

S-04

Building Section

1:50

KASHYAP HARISH VAGHANI

SCHOOL: KENCID

SCALE: 1:50

09/07/2024


REG: ARE/0171A/2023

BUILDING SECTION

3.300 1.800 1.800 2.200 3.000

skylight beam(50X150)
skylight glass bed beam(50X50)

BEAM 1(450X200)

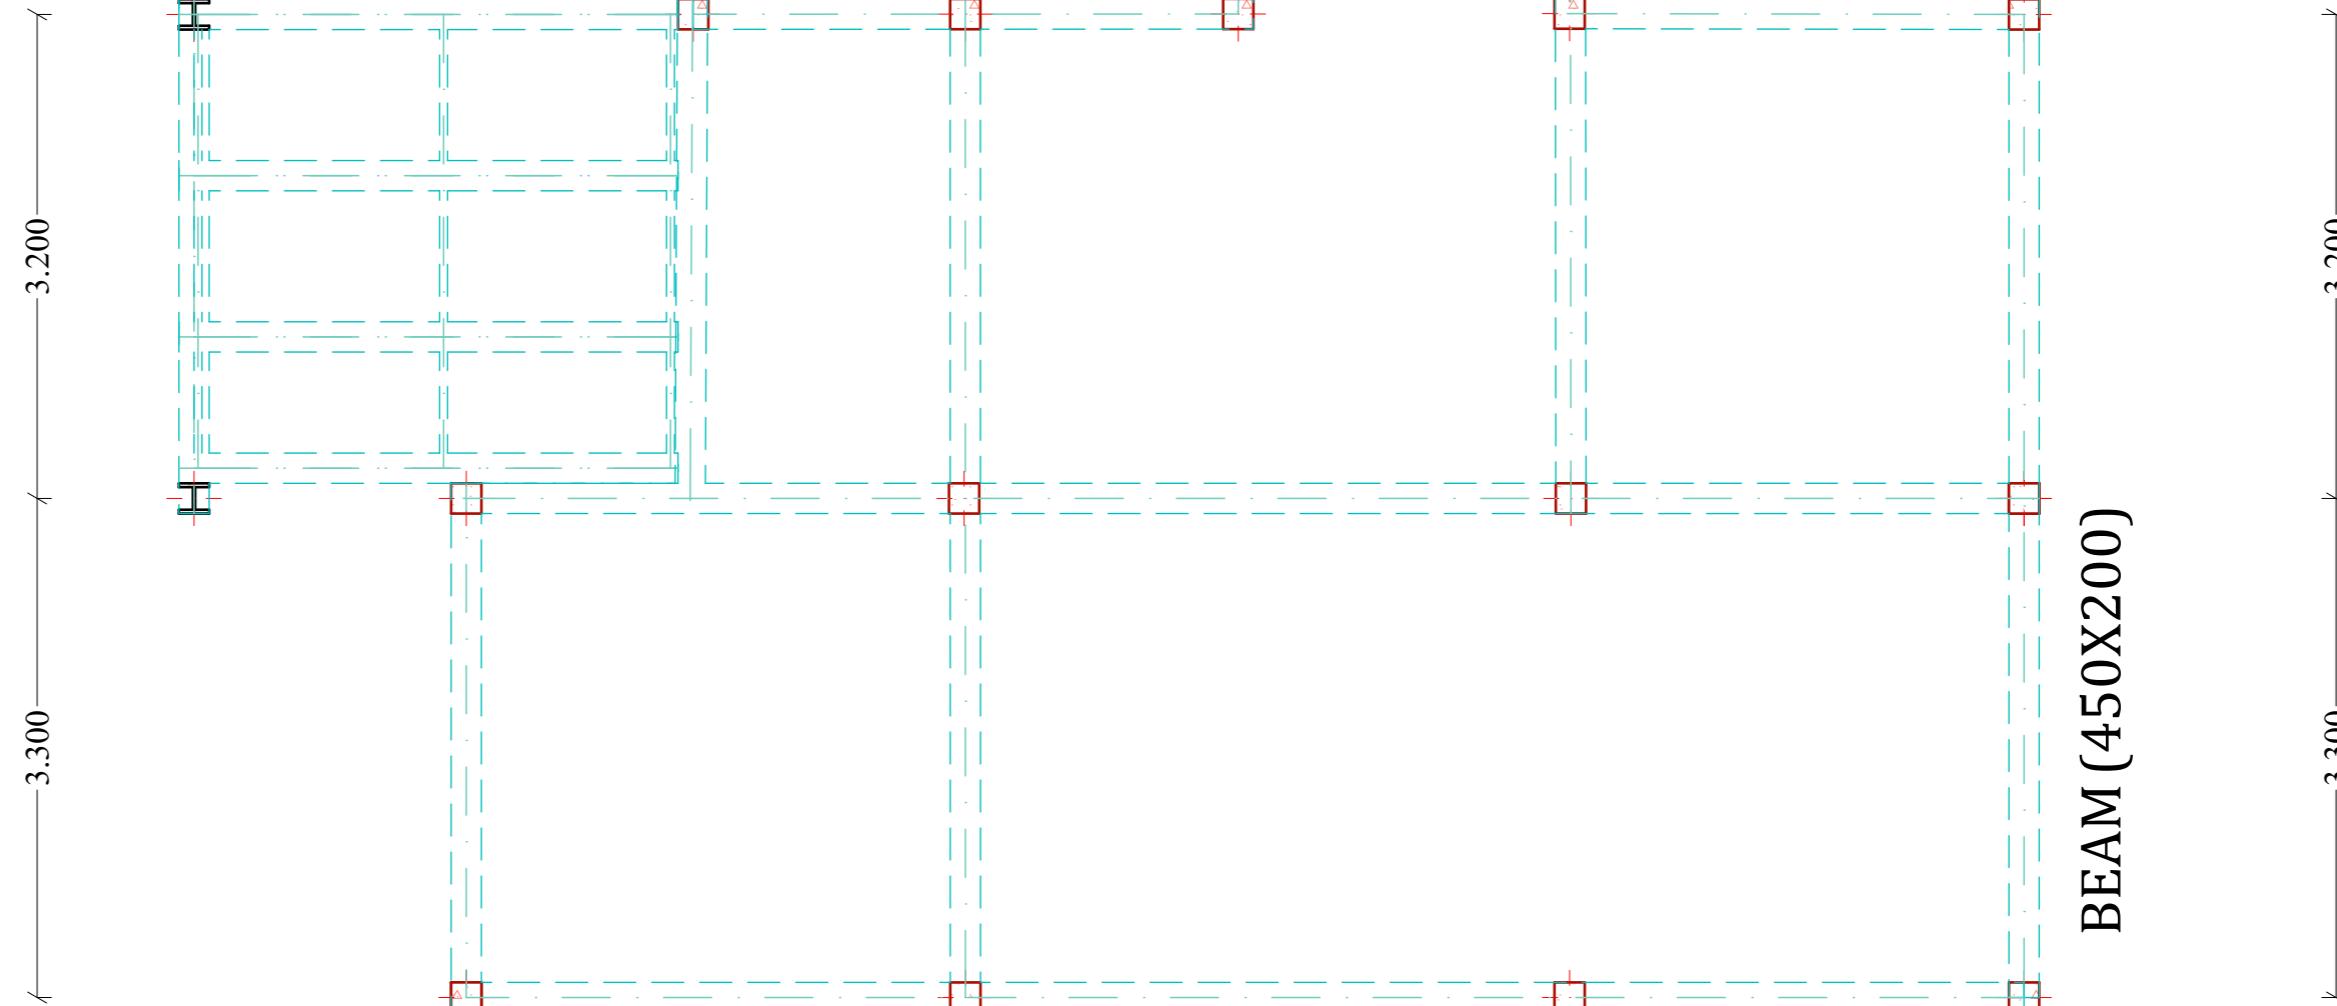

0. 3.300 4.000 3.000 1:50

Ground Floor

1ST FLOOR SLAB

KASHYAP HARISH VAGHANI


SCHOOL: KENCID

SCALE: 1:50

09/07/2024

REG: ARE/0171A/2023

DETAILED DRAWINGS

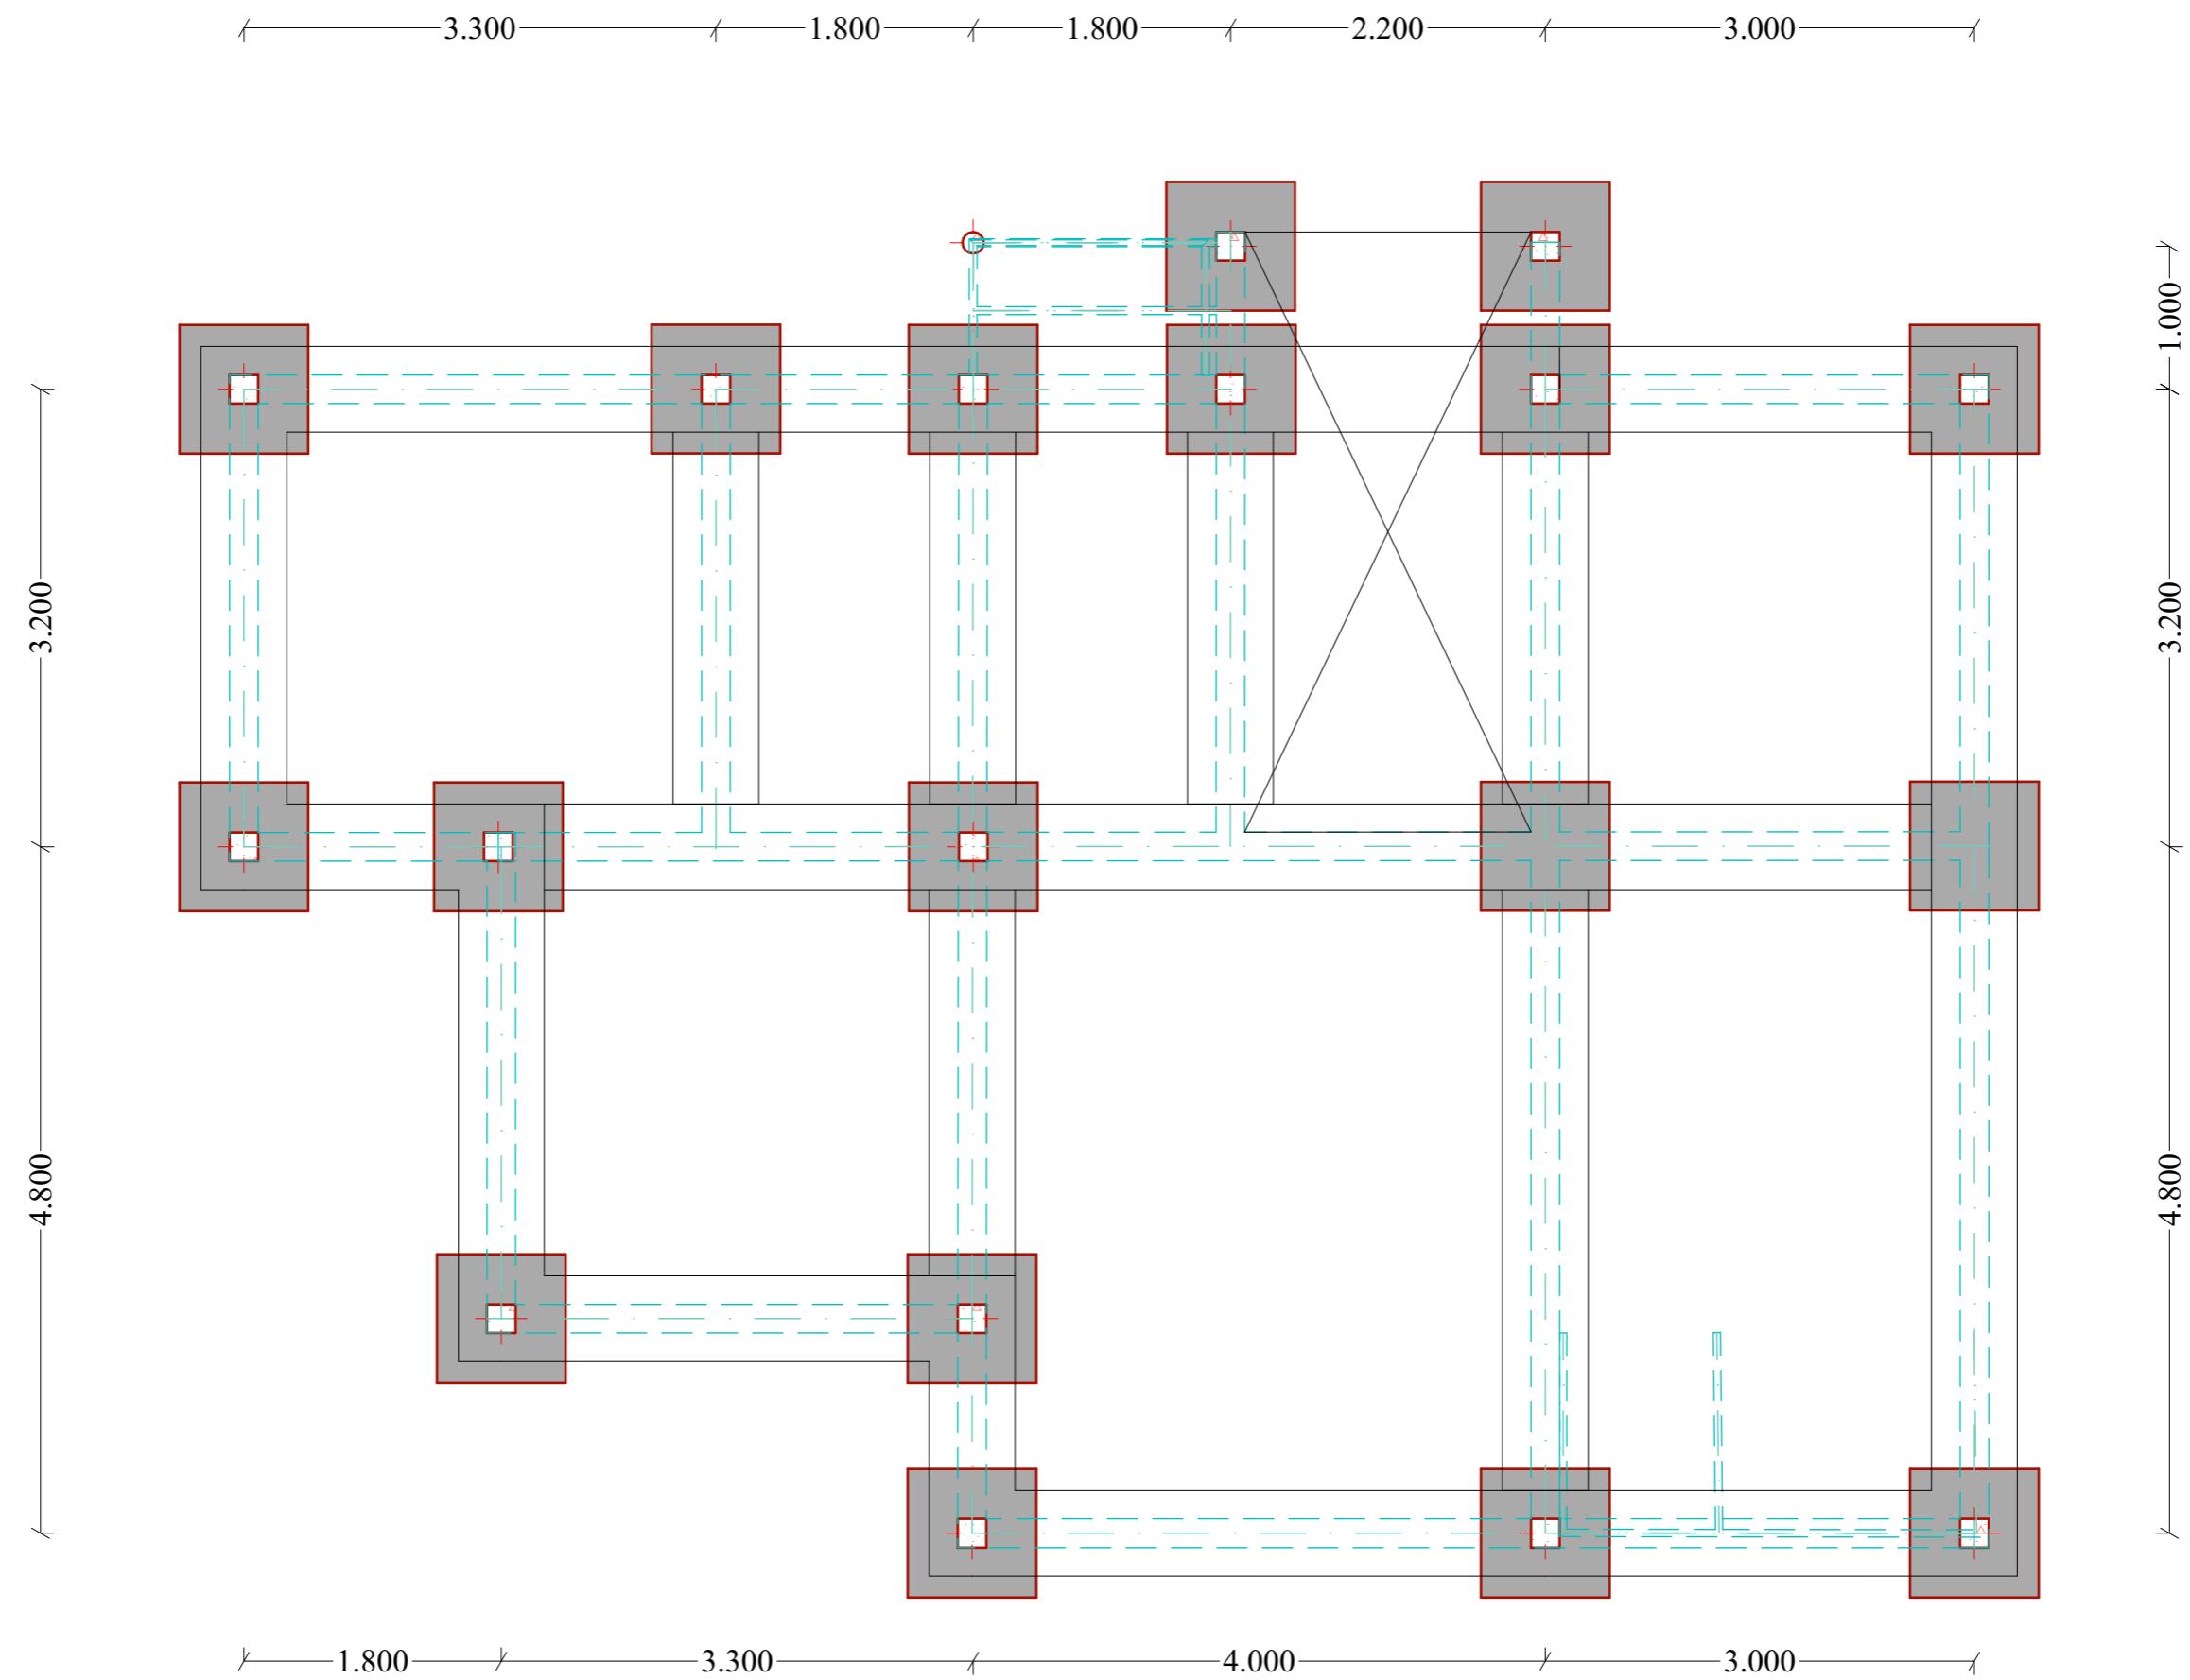

FOUNDATION LAYOUT

KASHYAP HARISH VAGHANI


SCHOOL: KENCID

SCALE: 1:50


09/07/2024

REG: ARE/0171A/2023


DETAILED DRAWINGS

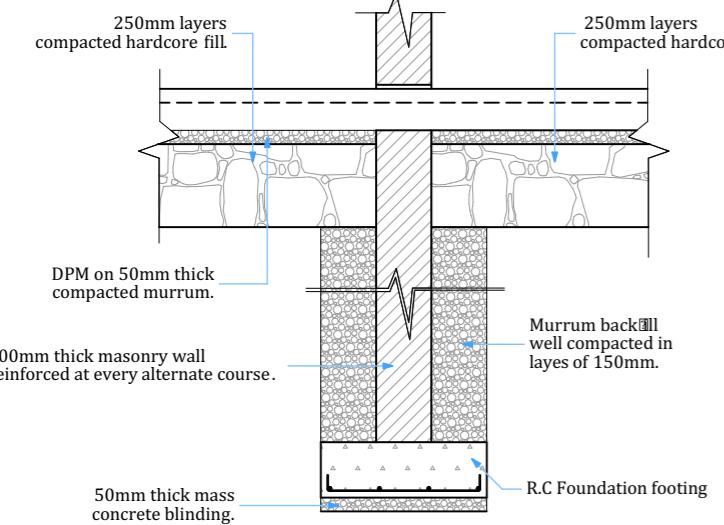

TYPICAL INTERNAL FOUNDATION WALLS

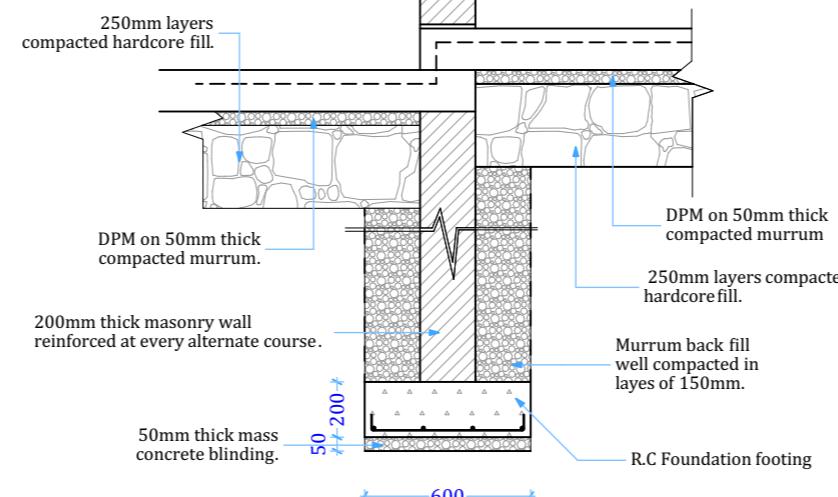

TYPICAL AT EXTERNAL OPENING FOUNDATION WALLS

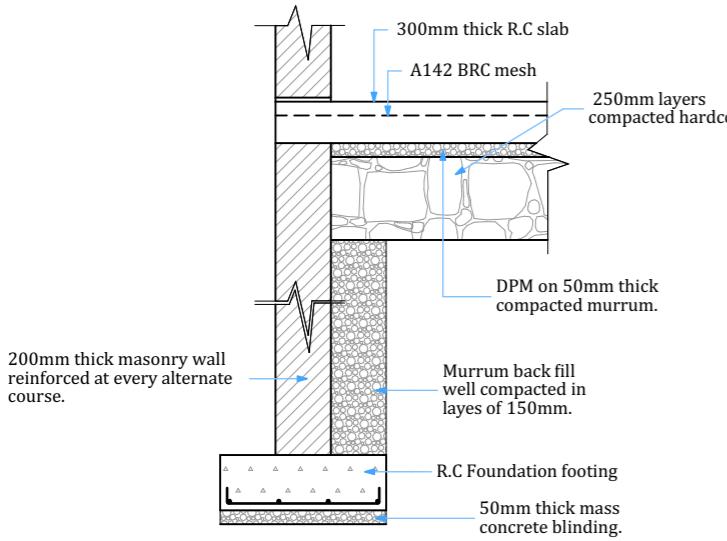


TYPICAL EXTERNAL FOUNDATION WALLS

200


SECTION R-R
SCALE 1:25

200


SECTION P-P
SCALE 1:25

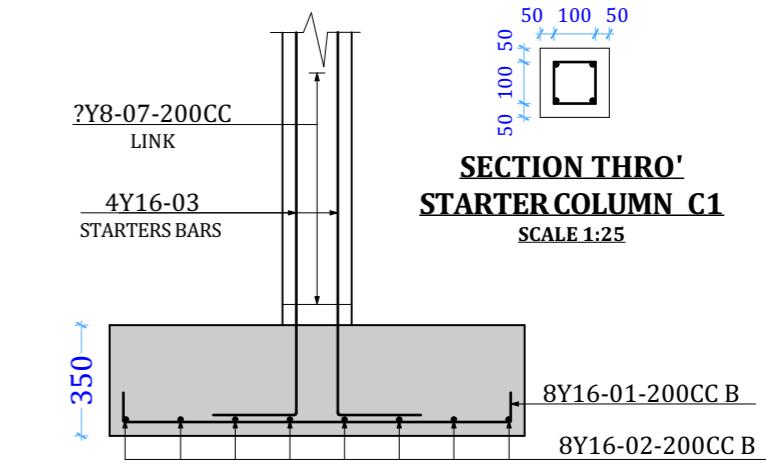


SECTION THRO' STARTER COLUMN C1
SCALE 1:25

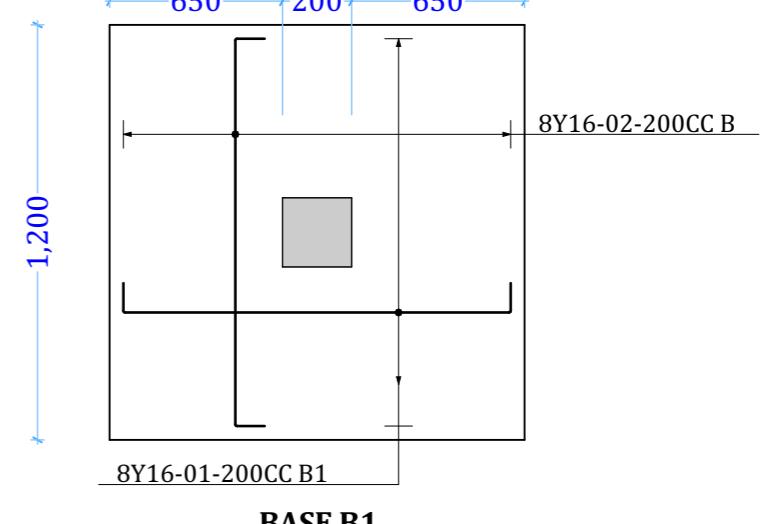





SECTION B1-B1
SCALE 1:25

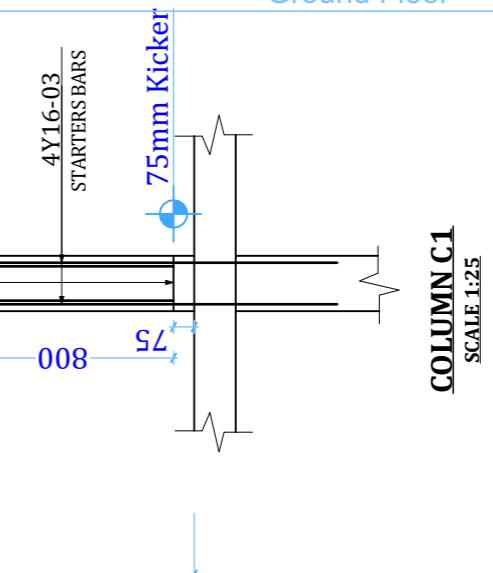


BASE B1
SCALE 1:25

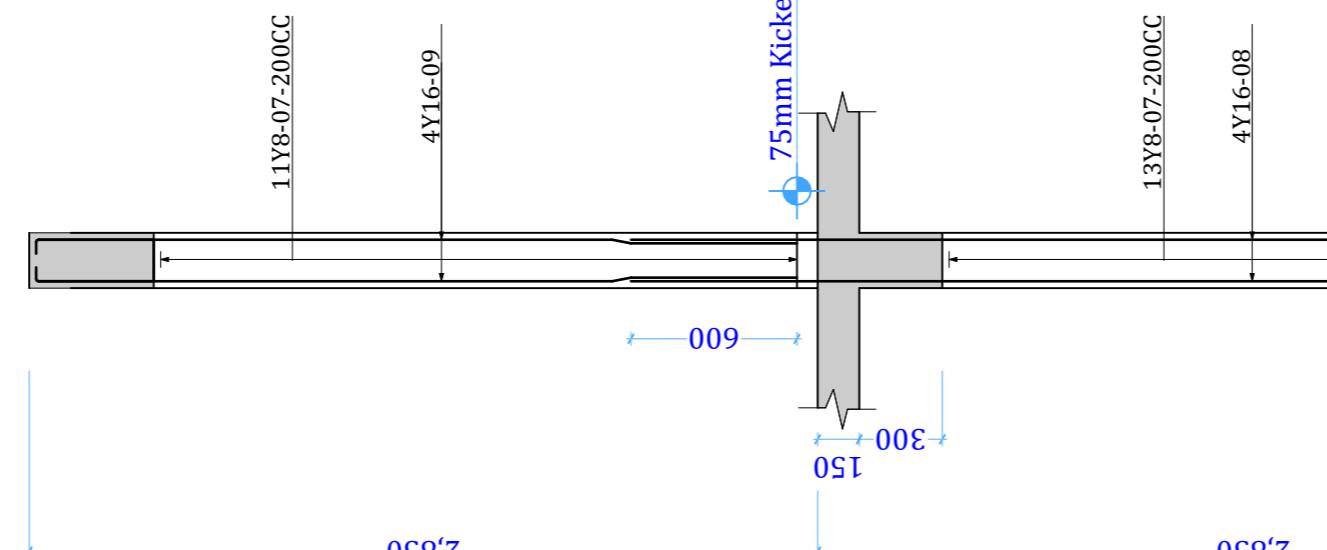

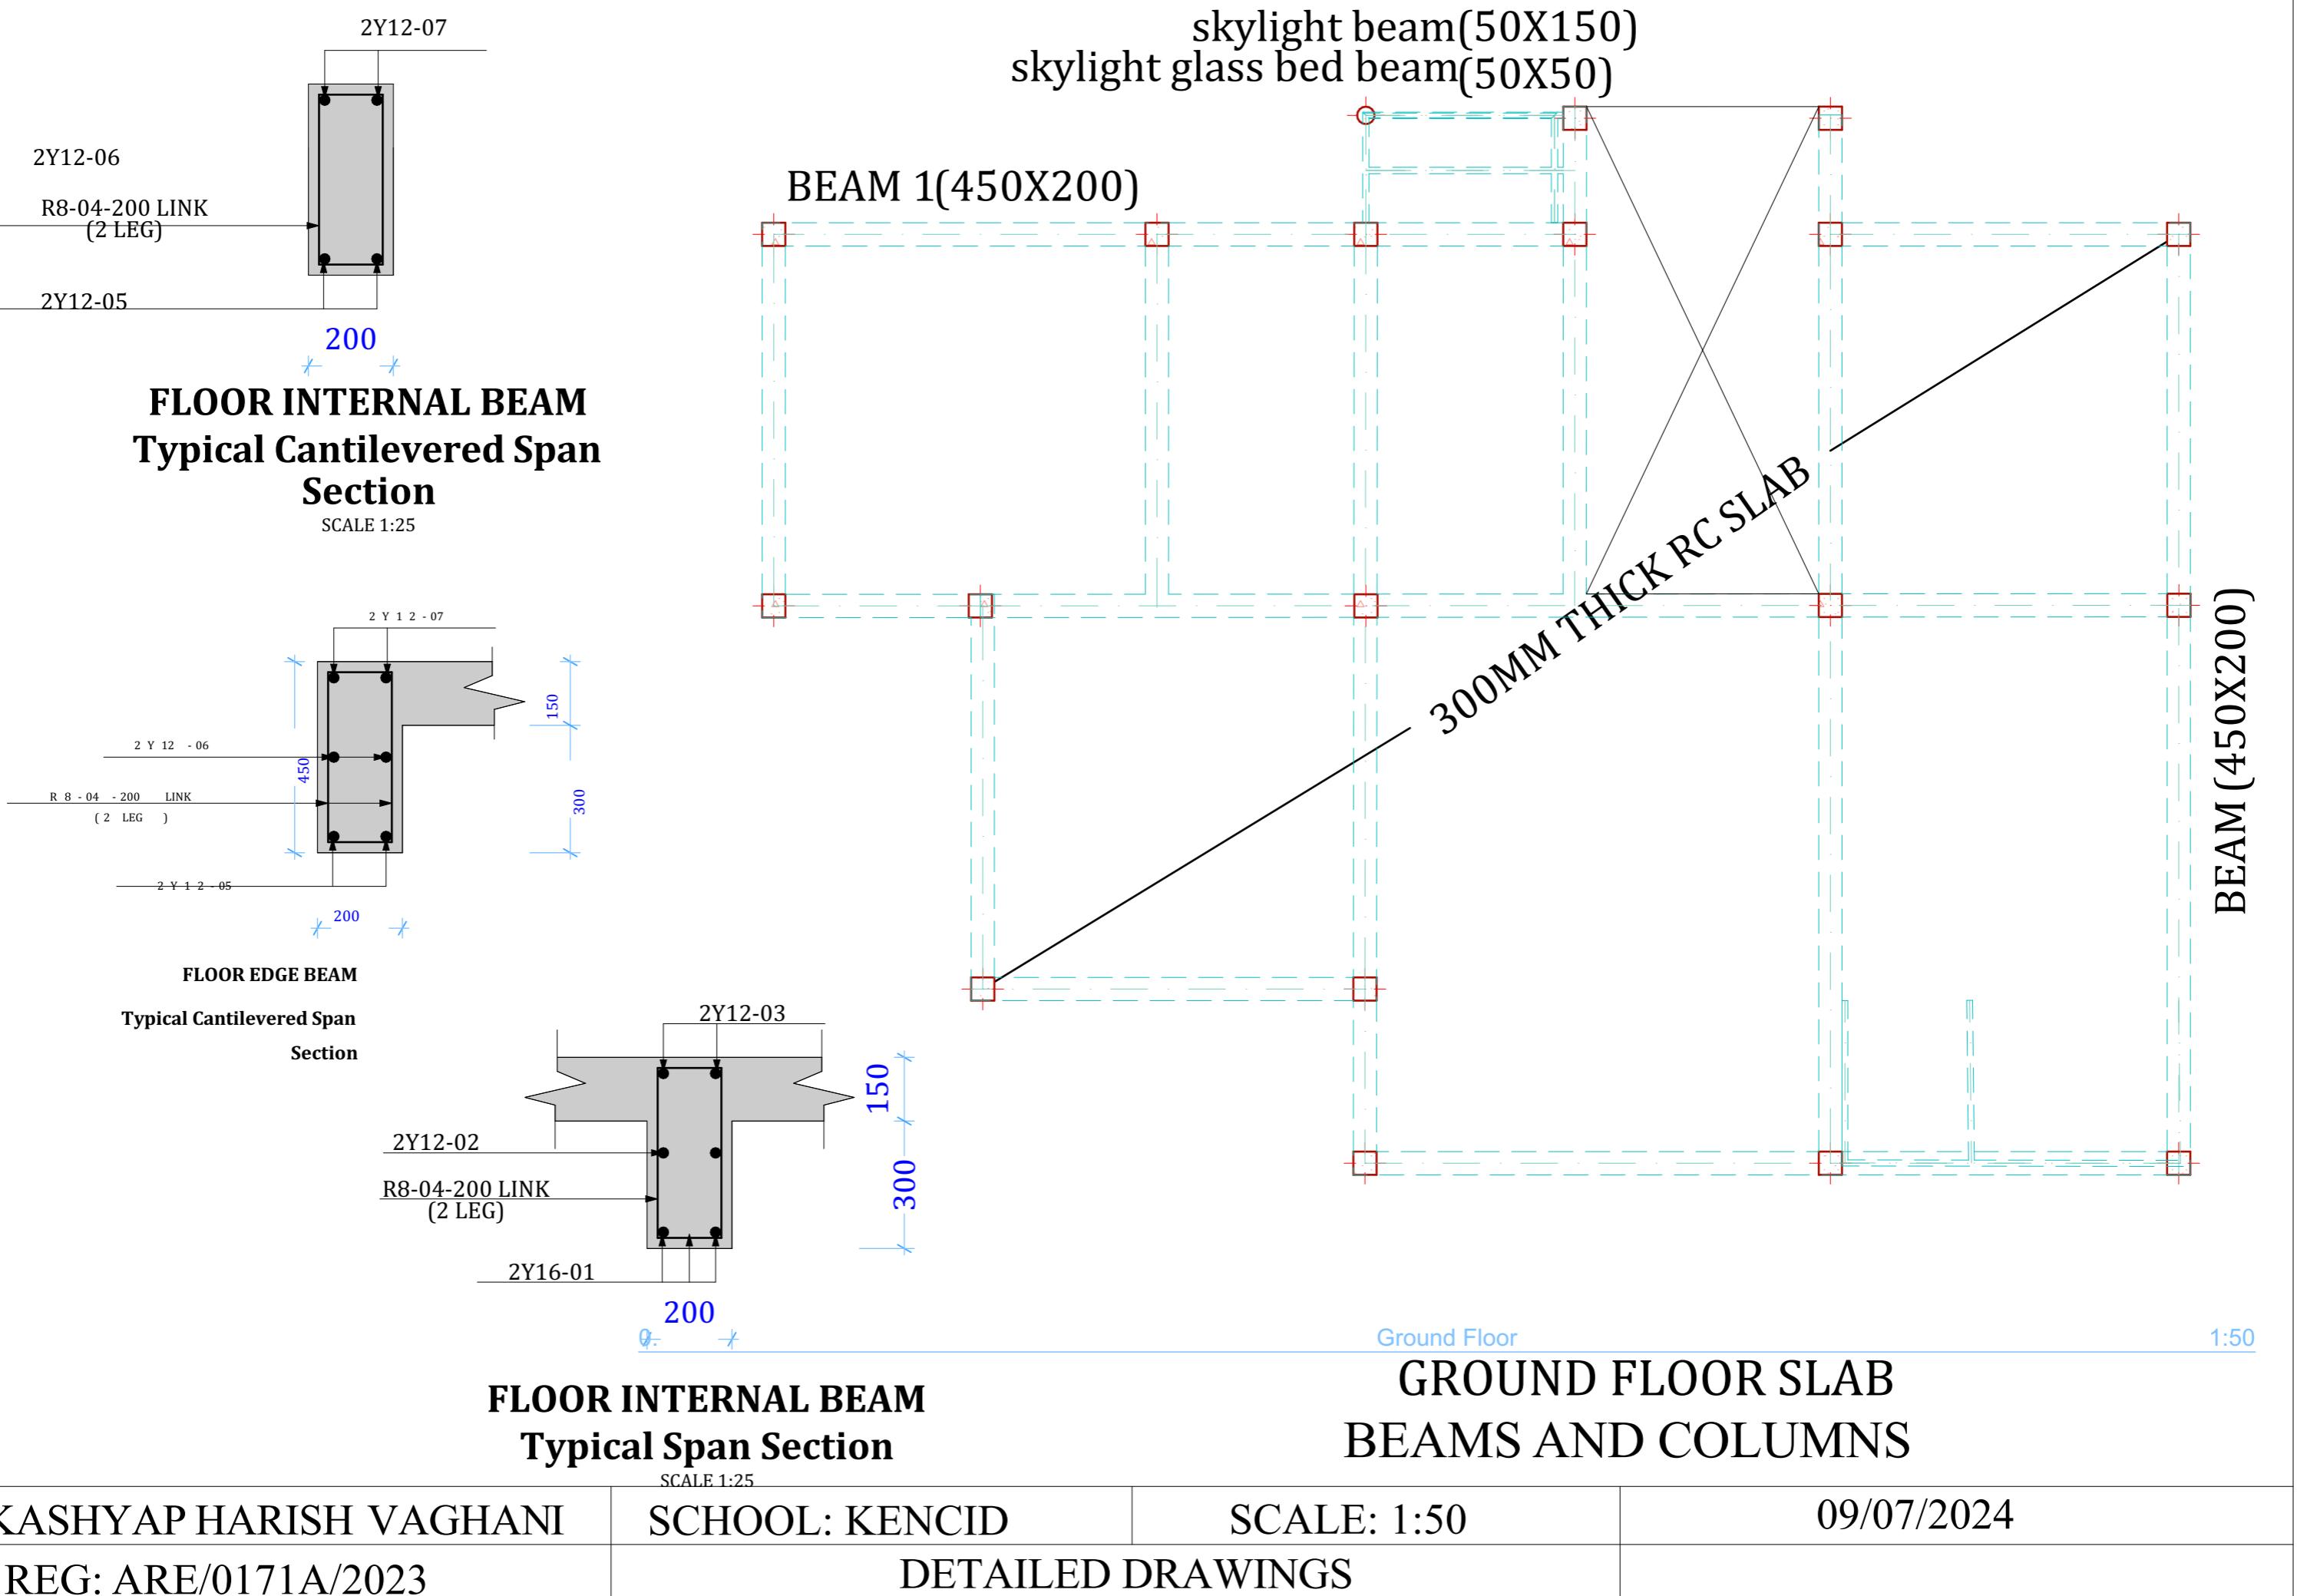

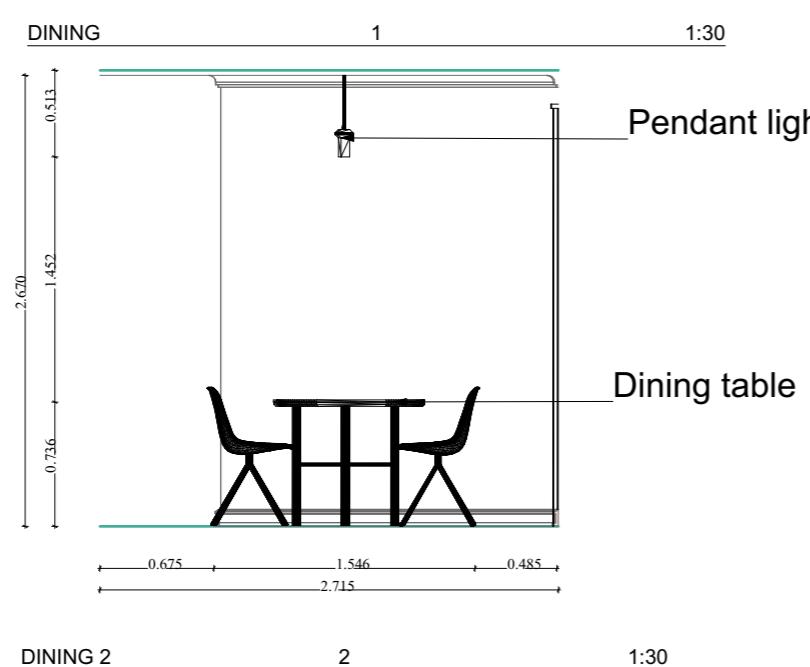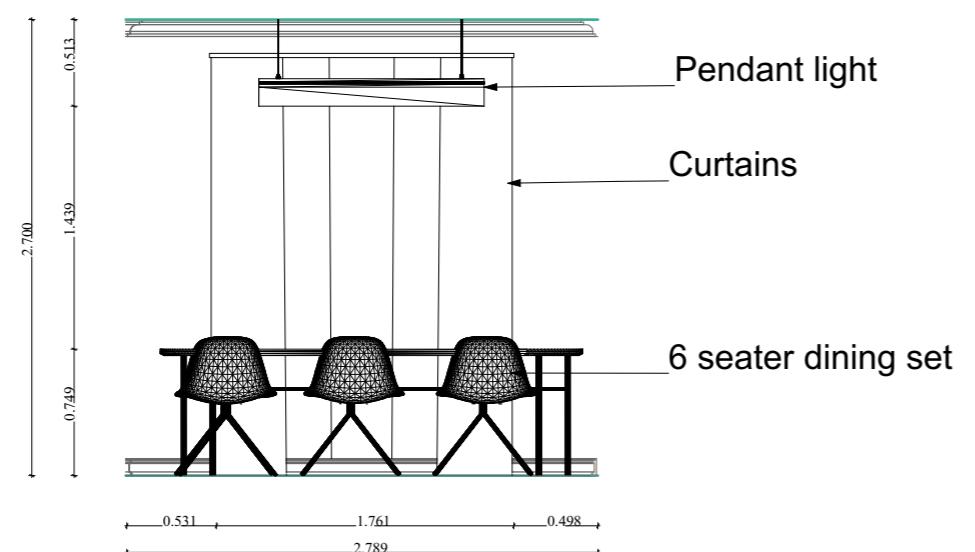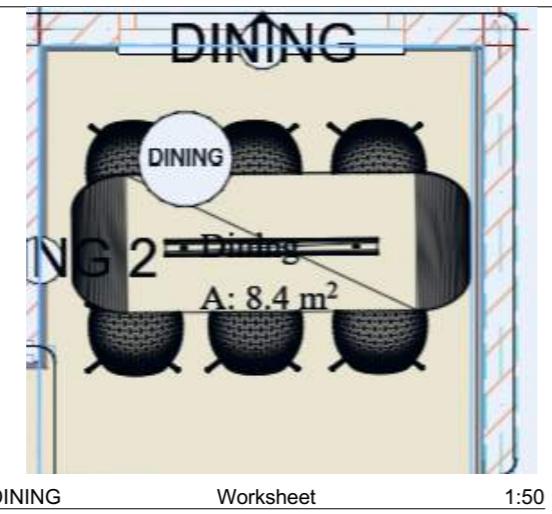

RENDERS

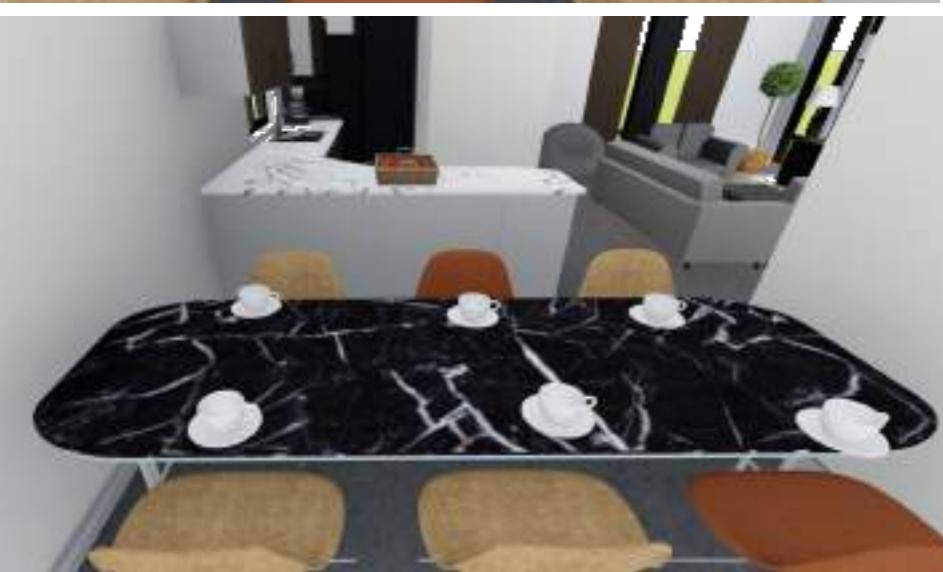

NAME: KASHYAB HARISH VAGHANI

REG NO: ARE/0171A/2023


SCHOOL: KENCID

DATE: 4/07/2024

UNITS: MILLIMETERS

SCALE: 1:30

DRAWING TITLE: 1, 2

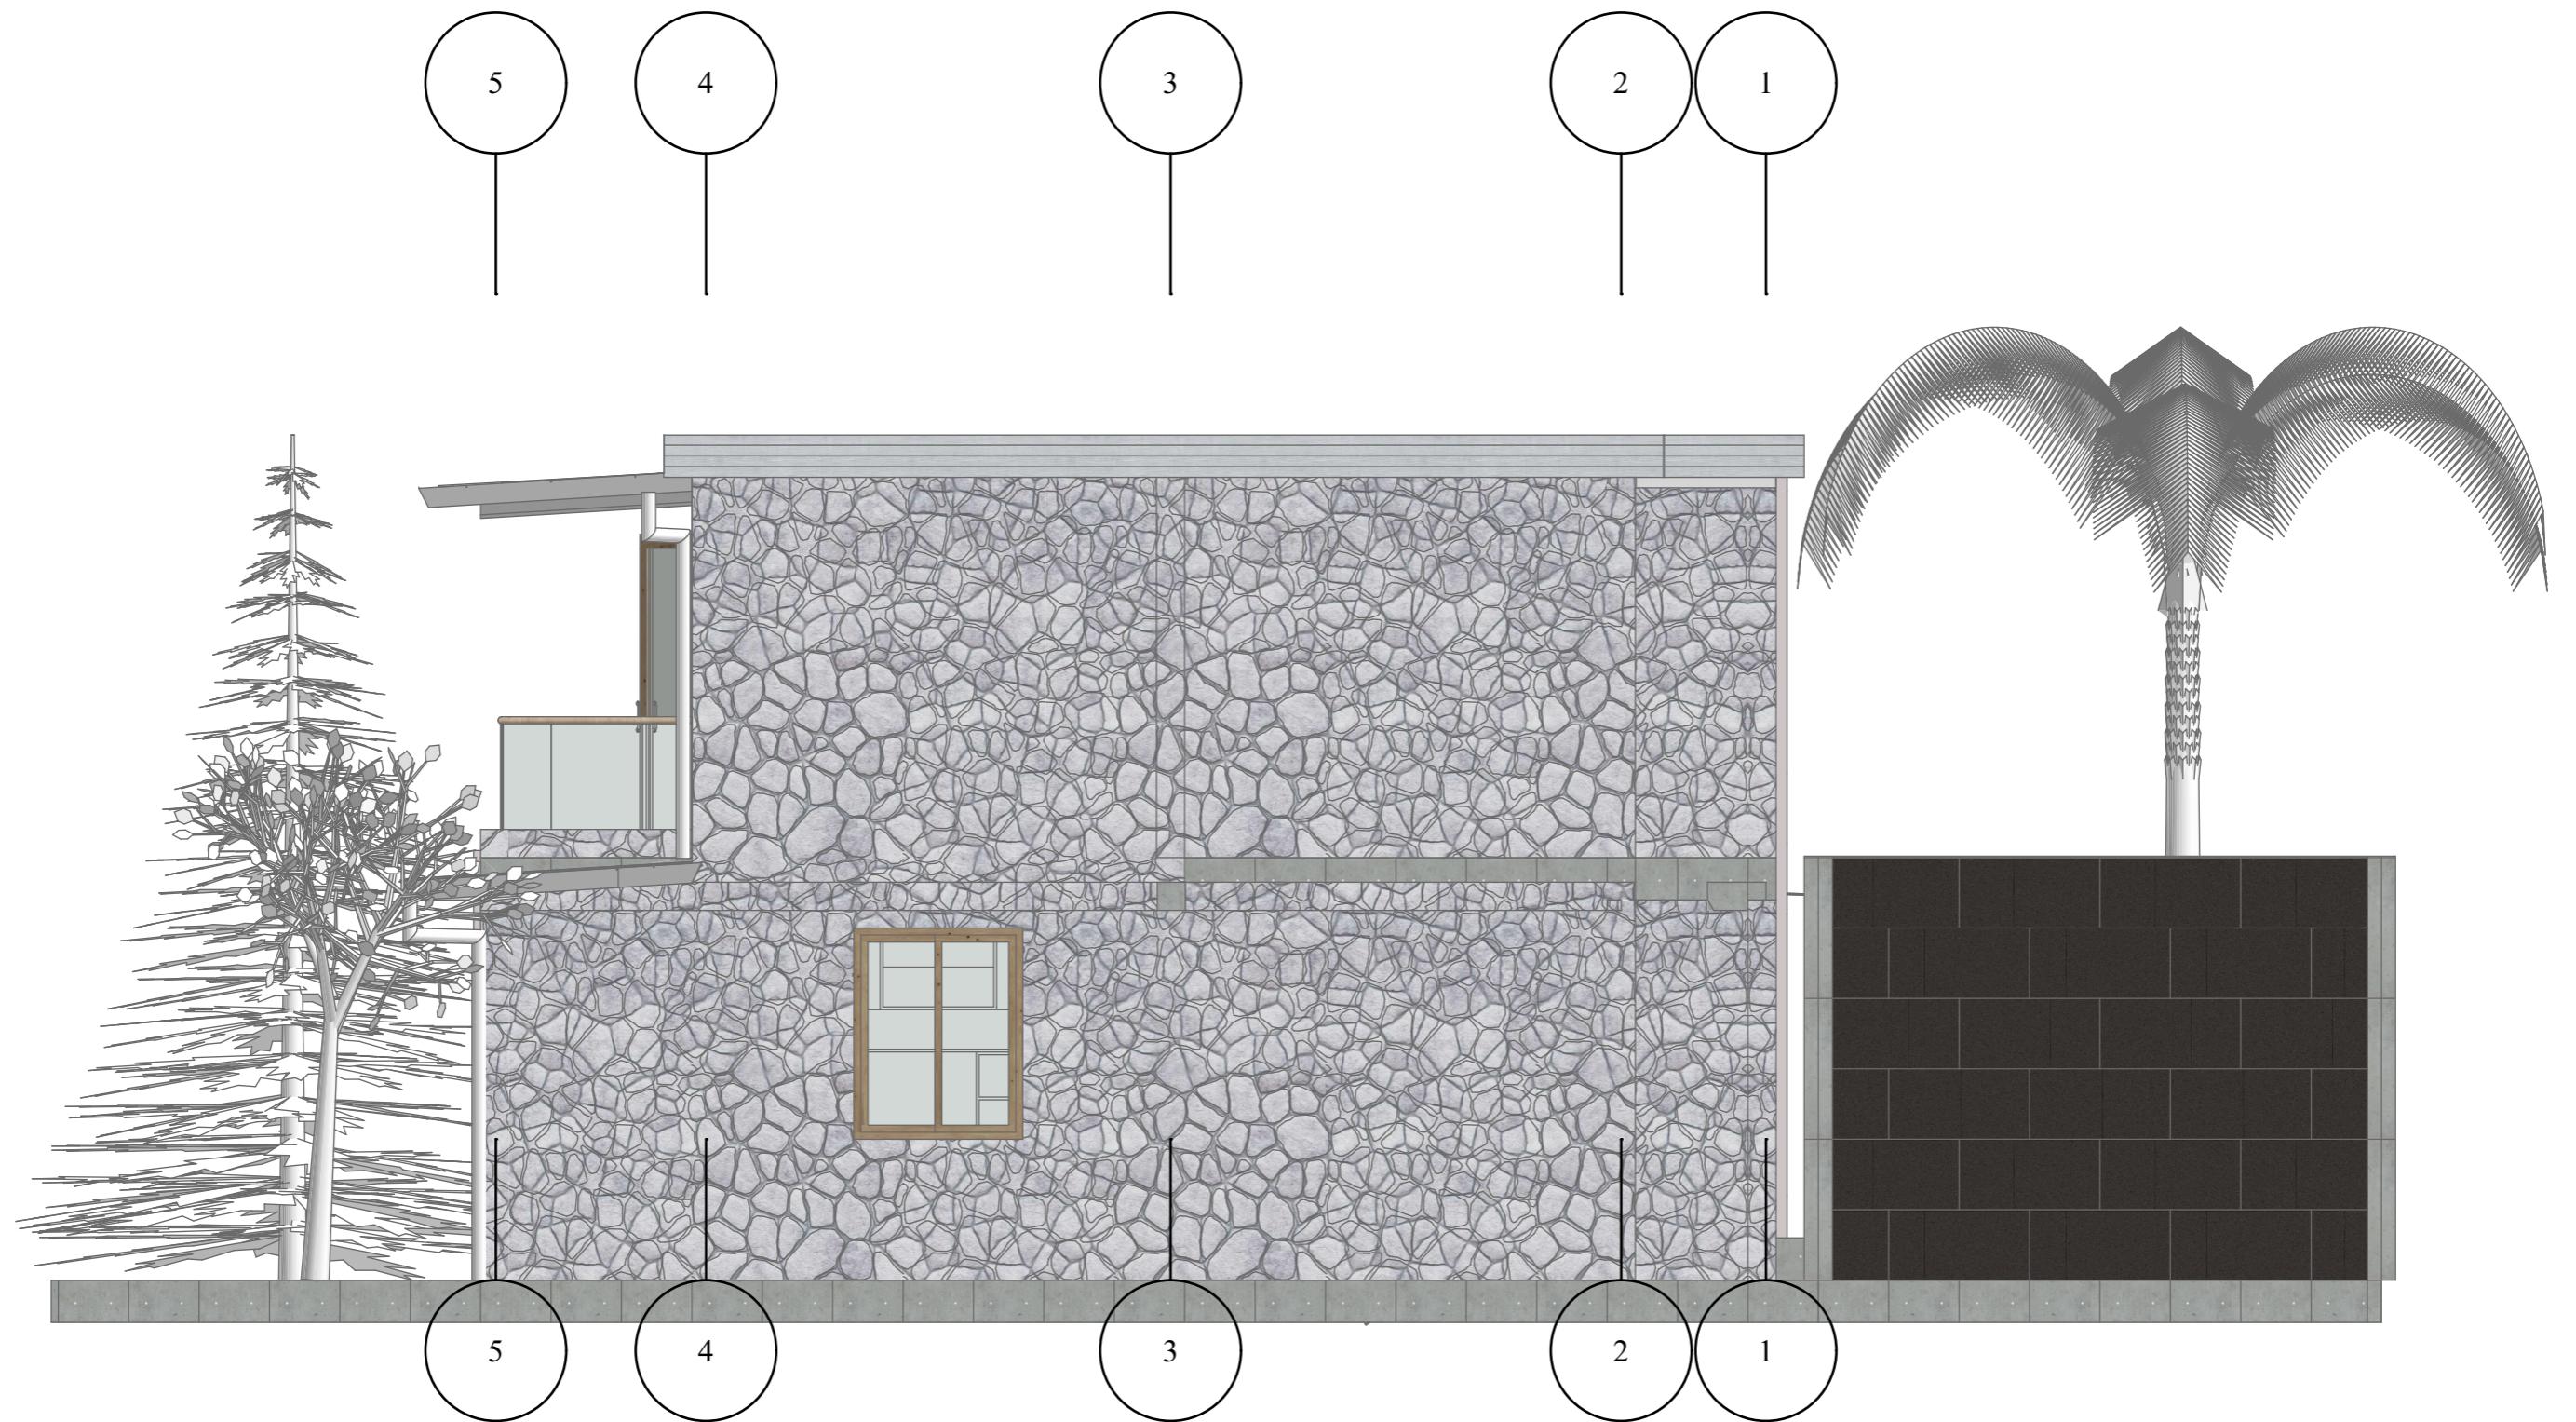

1.492 3.300 3.200 1.028

East Elevation

1:50

KASHYAP HARISH VAGHANI

REG: ARE/0171A/2023


SCHOOL: KENCID

EAST ELEVATION



SCALE: 1:50

09/07/2024

North Elevation △

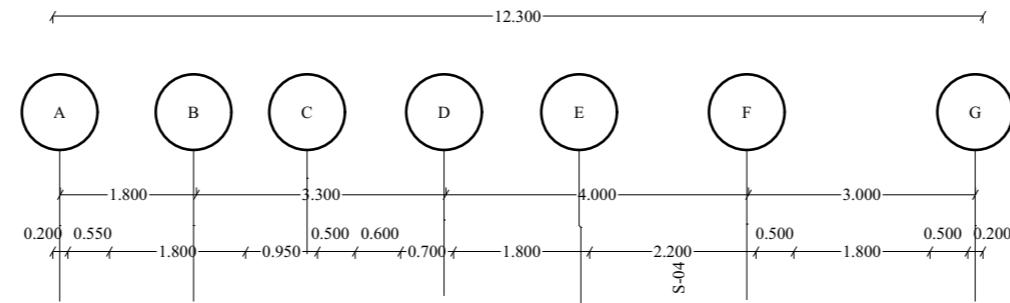

↙ West Elevation

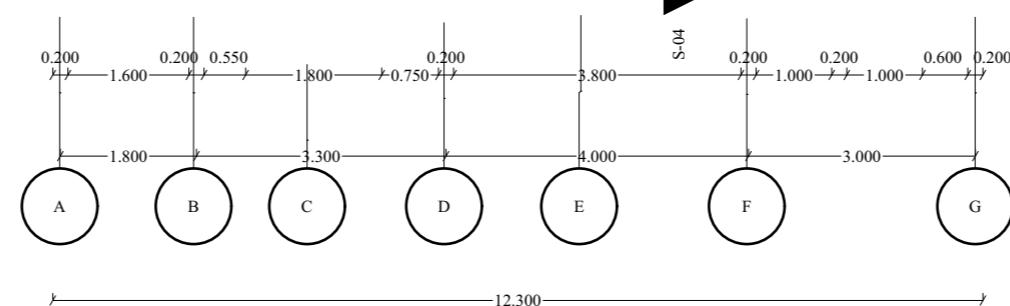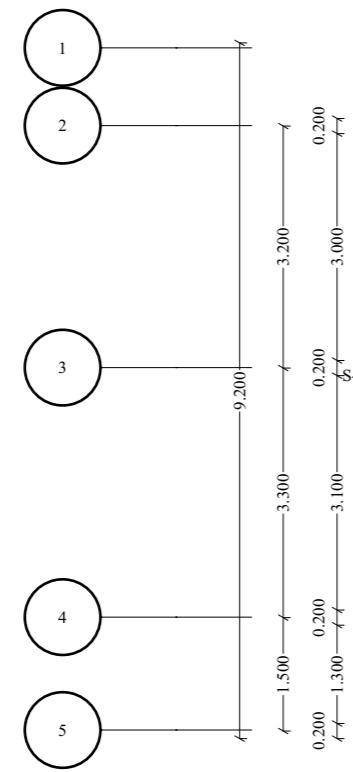

Ground Floor

1:100

South Elevation ▲

KASHYAP HARISH VAGHANI



SCHOOL: KENCID

SCALE: 1:100

FRIST FLOOR PLAN

REG: ARE/0171A/2023

20/02/2023

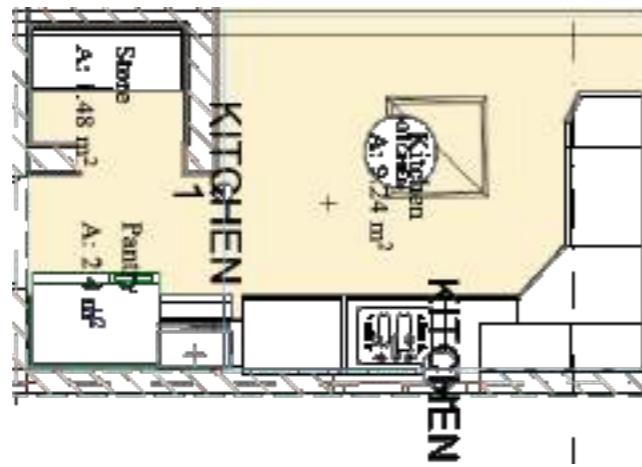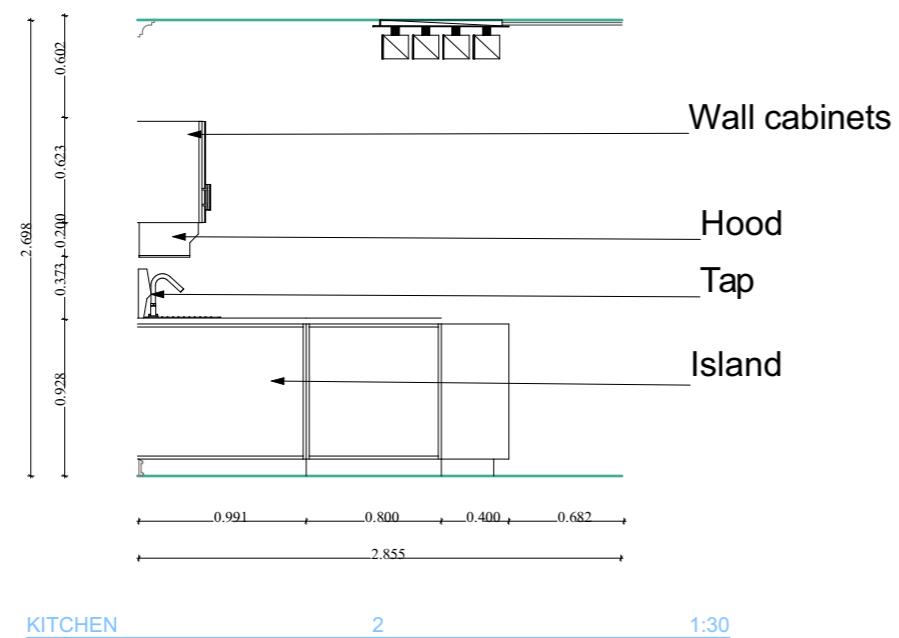WORKSHEET**ELEVATIONS**

NAME: KASHYAP HARISH VAGHANI

REG NO: ARE/0171A/2023

SCHOOL: KENCID

DATE: 4/07/2024

UNITS: MILLIMETERS

SCALE:1:30

DRAWING TITLE:1, 2





3.020 2.194 1.809 1.811 1.501 1.781

North Elevation

1:51.28

KASHYAP HARISH VAGHANI


SCHOOL: KENCID

SCALE: 1:50

09/07/2024

REG: ARE/0171A/2023

NORTH ELEVATION

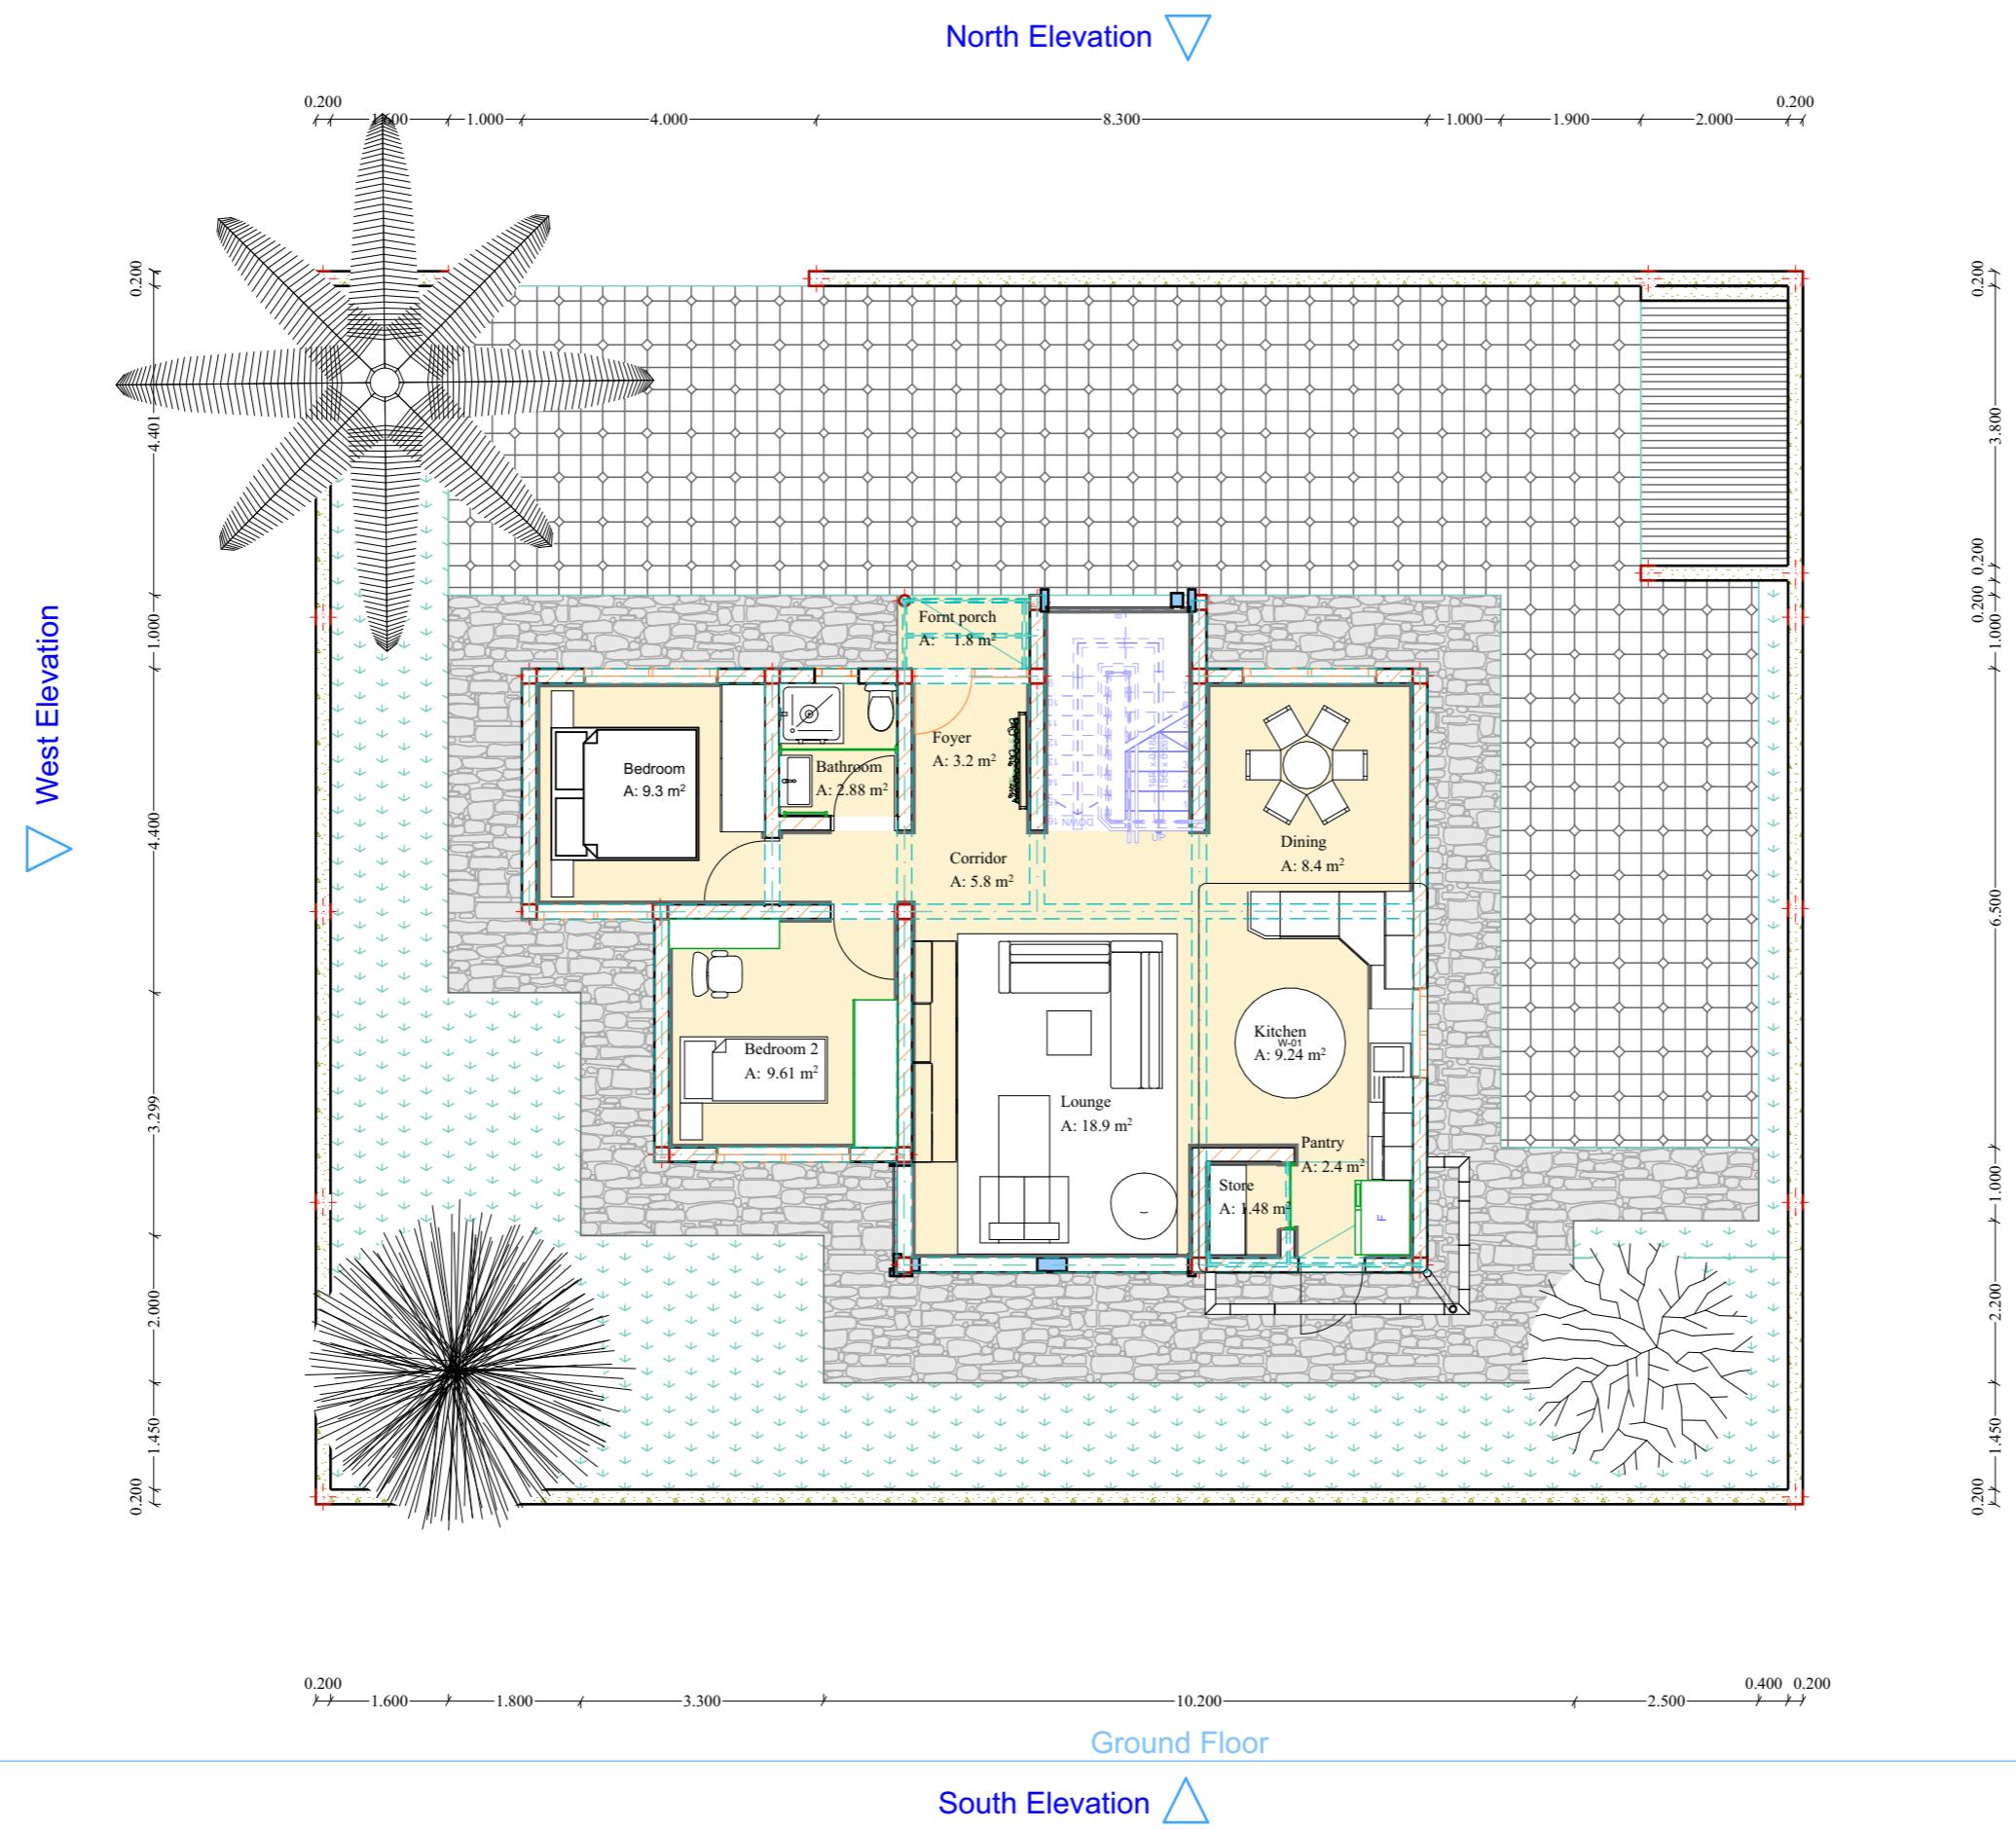

KASHYAP HARISH VAGHANI

SCHOOL: KENCID


REG: ARE/0171A/2023

SCALE: 1:100

SITE PLAN

09/07/2024

1:100

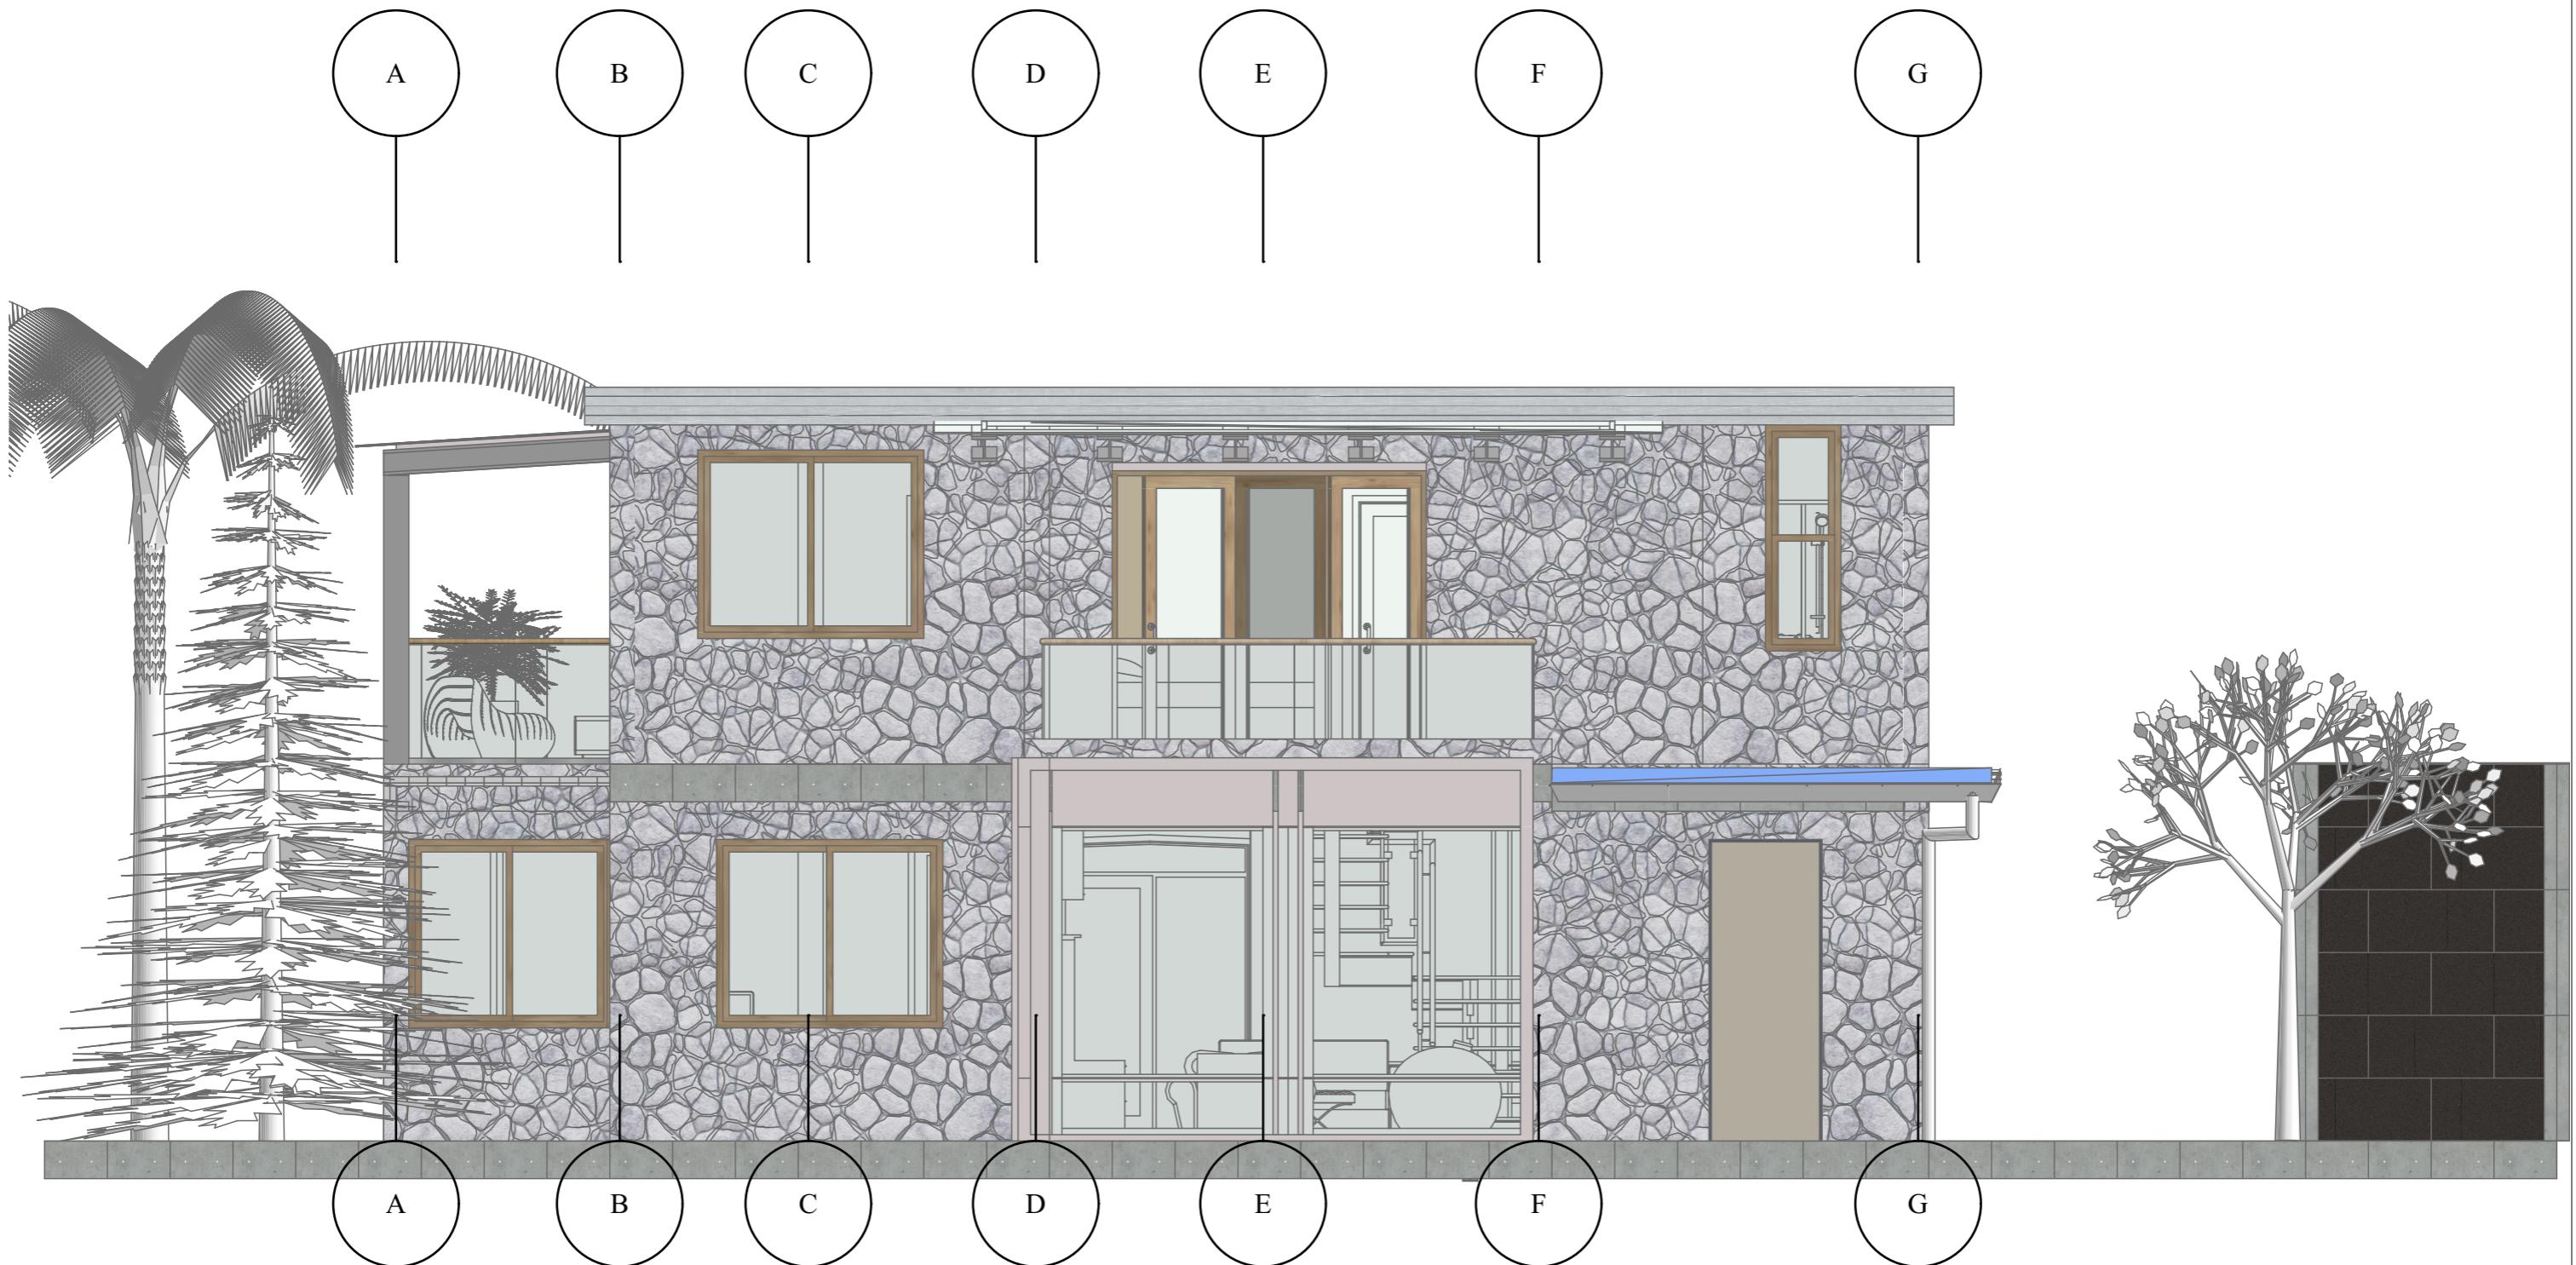

South Elevation

1:51.28

KASHYAP HARISH VAGHANI


REG: ARE/0171A/2023

SCHOOL: KENCID

SOUTH ELEVATION

SCALE: 1:50

09/07/2024

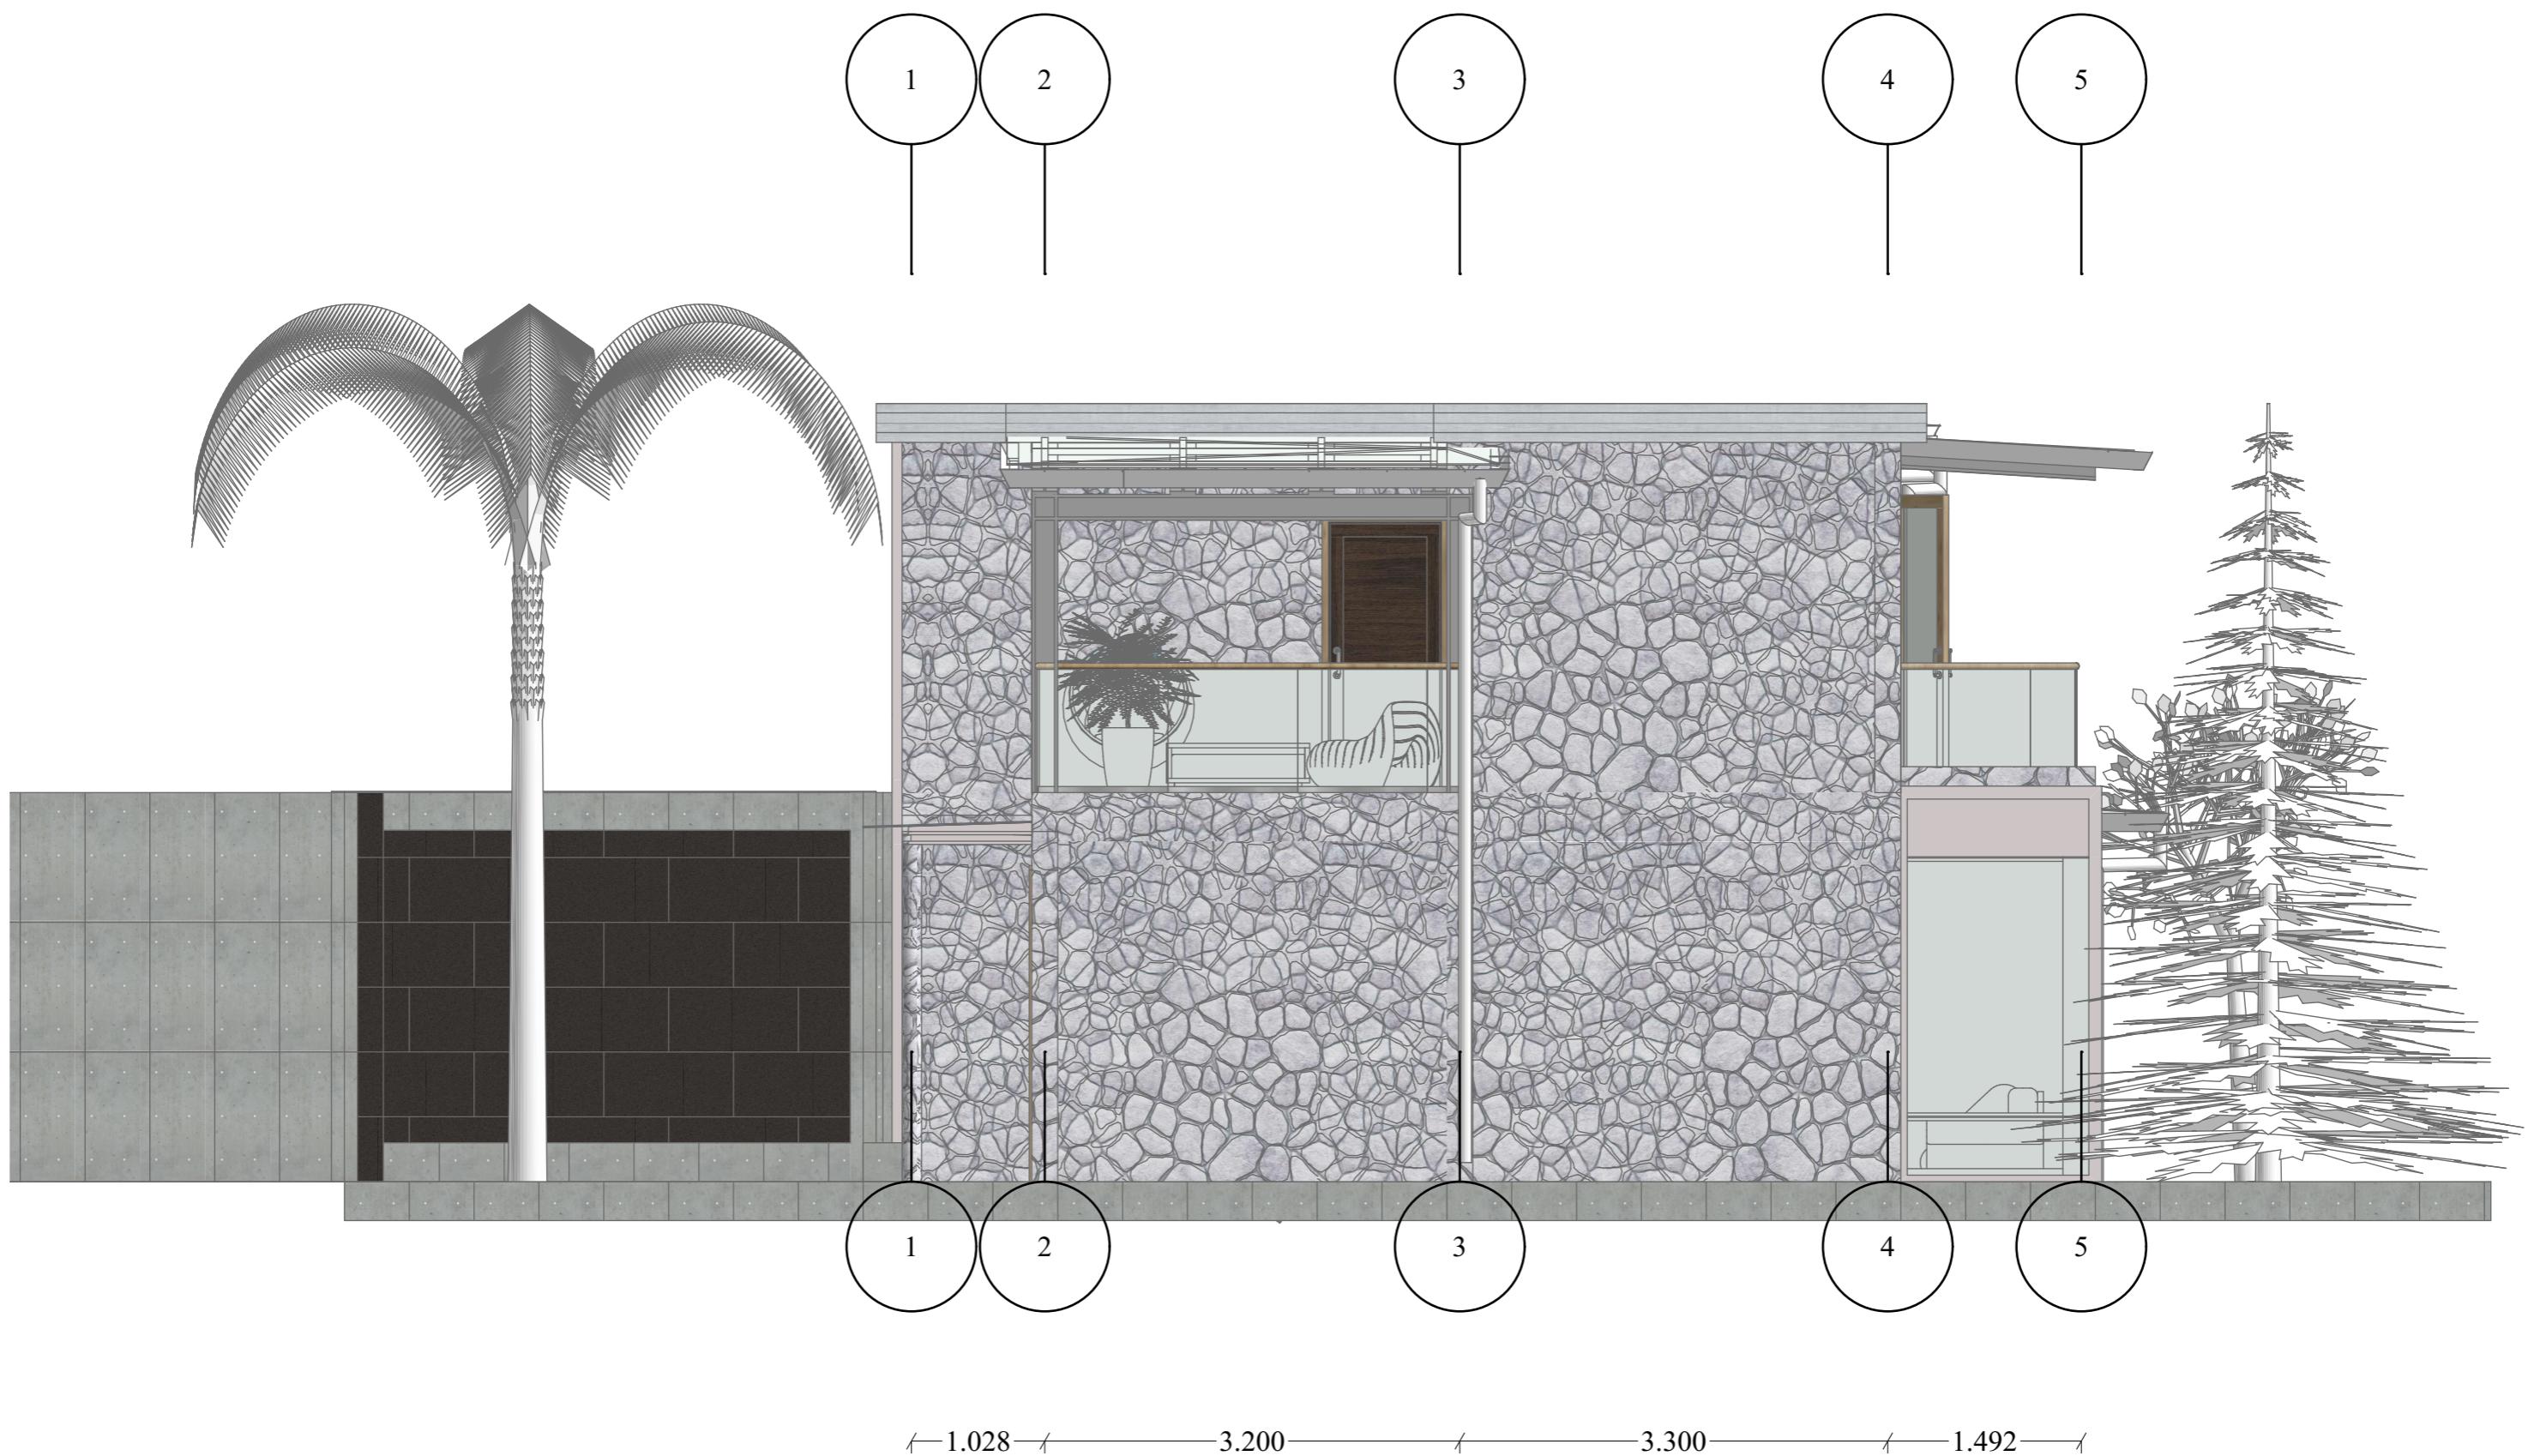

1

West Elevation

1:50

KASHYAP HARISH VAGHANI


SCHOOL: KENCID

SCALE: 1:50

09/07/2024

REG: ARE/0171A/2023

WEST ELEVATION

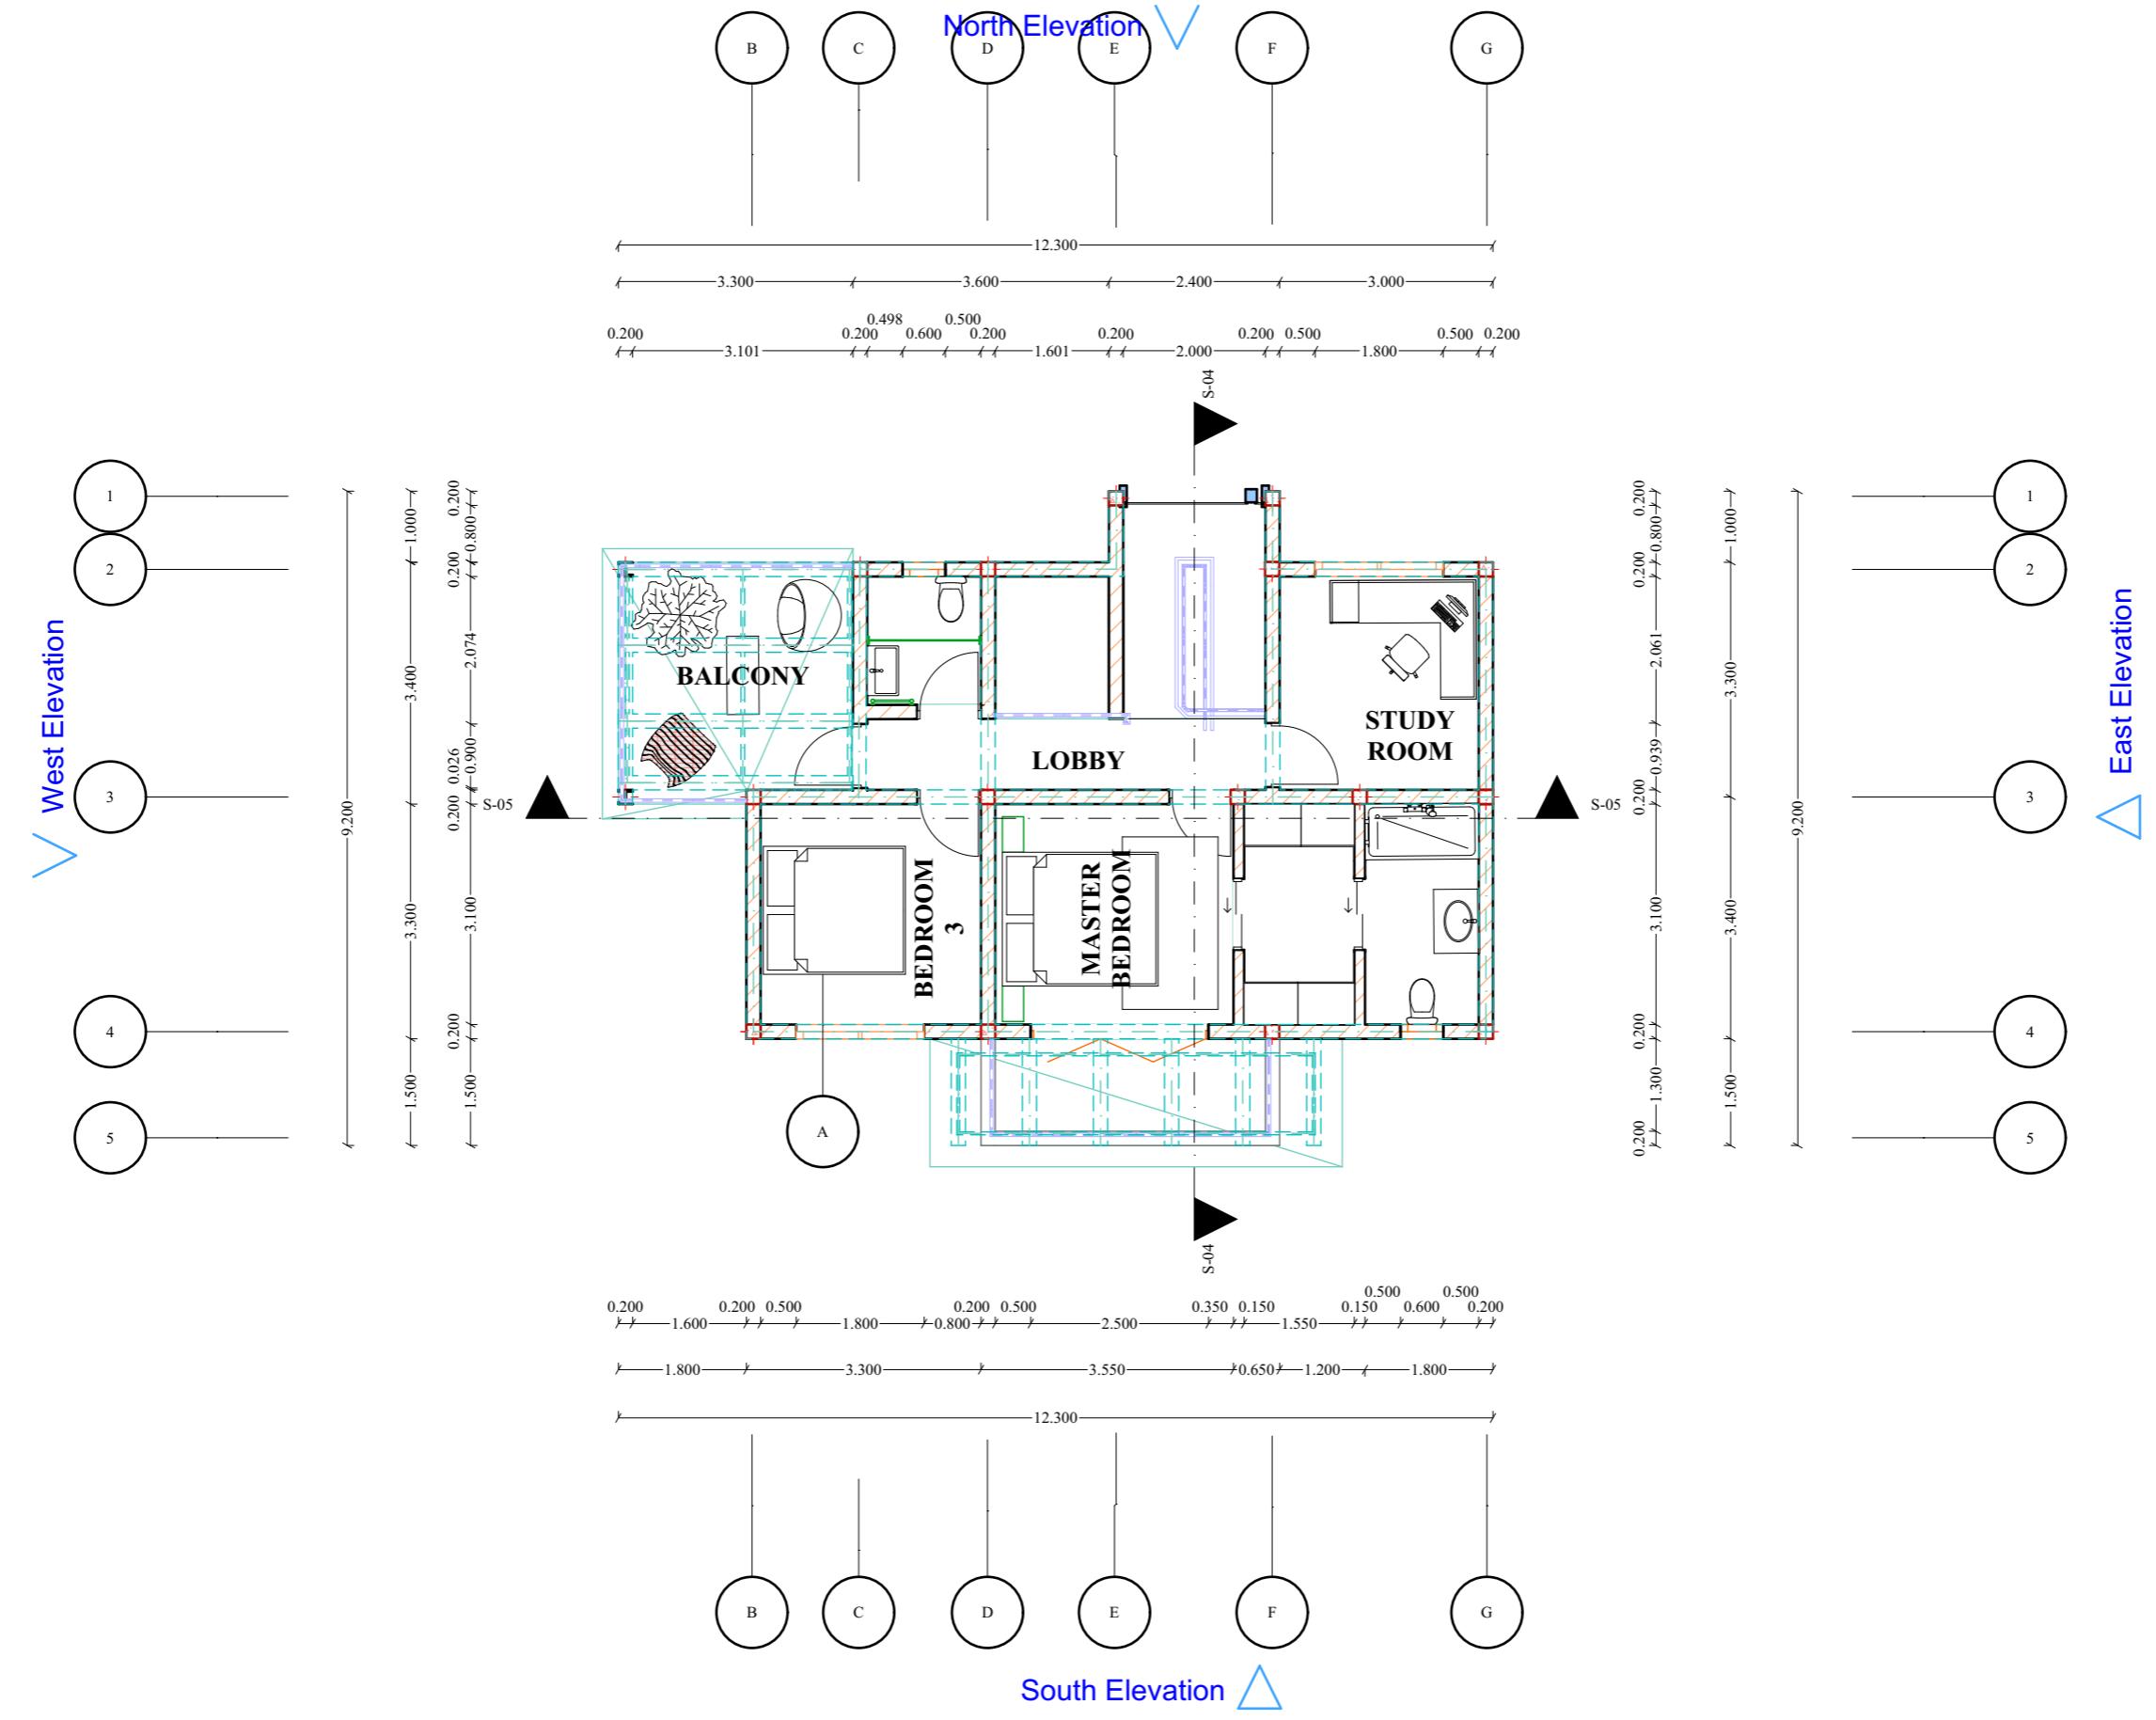

1.

1:100

KASHYAP HARISH VAGHANI


SCHOOL: KENCID

SCALE: 1:100

FRIST FLOOR PLAN

REG: ARE/0171A/2023

09/07/2024

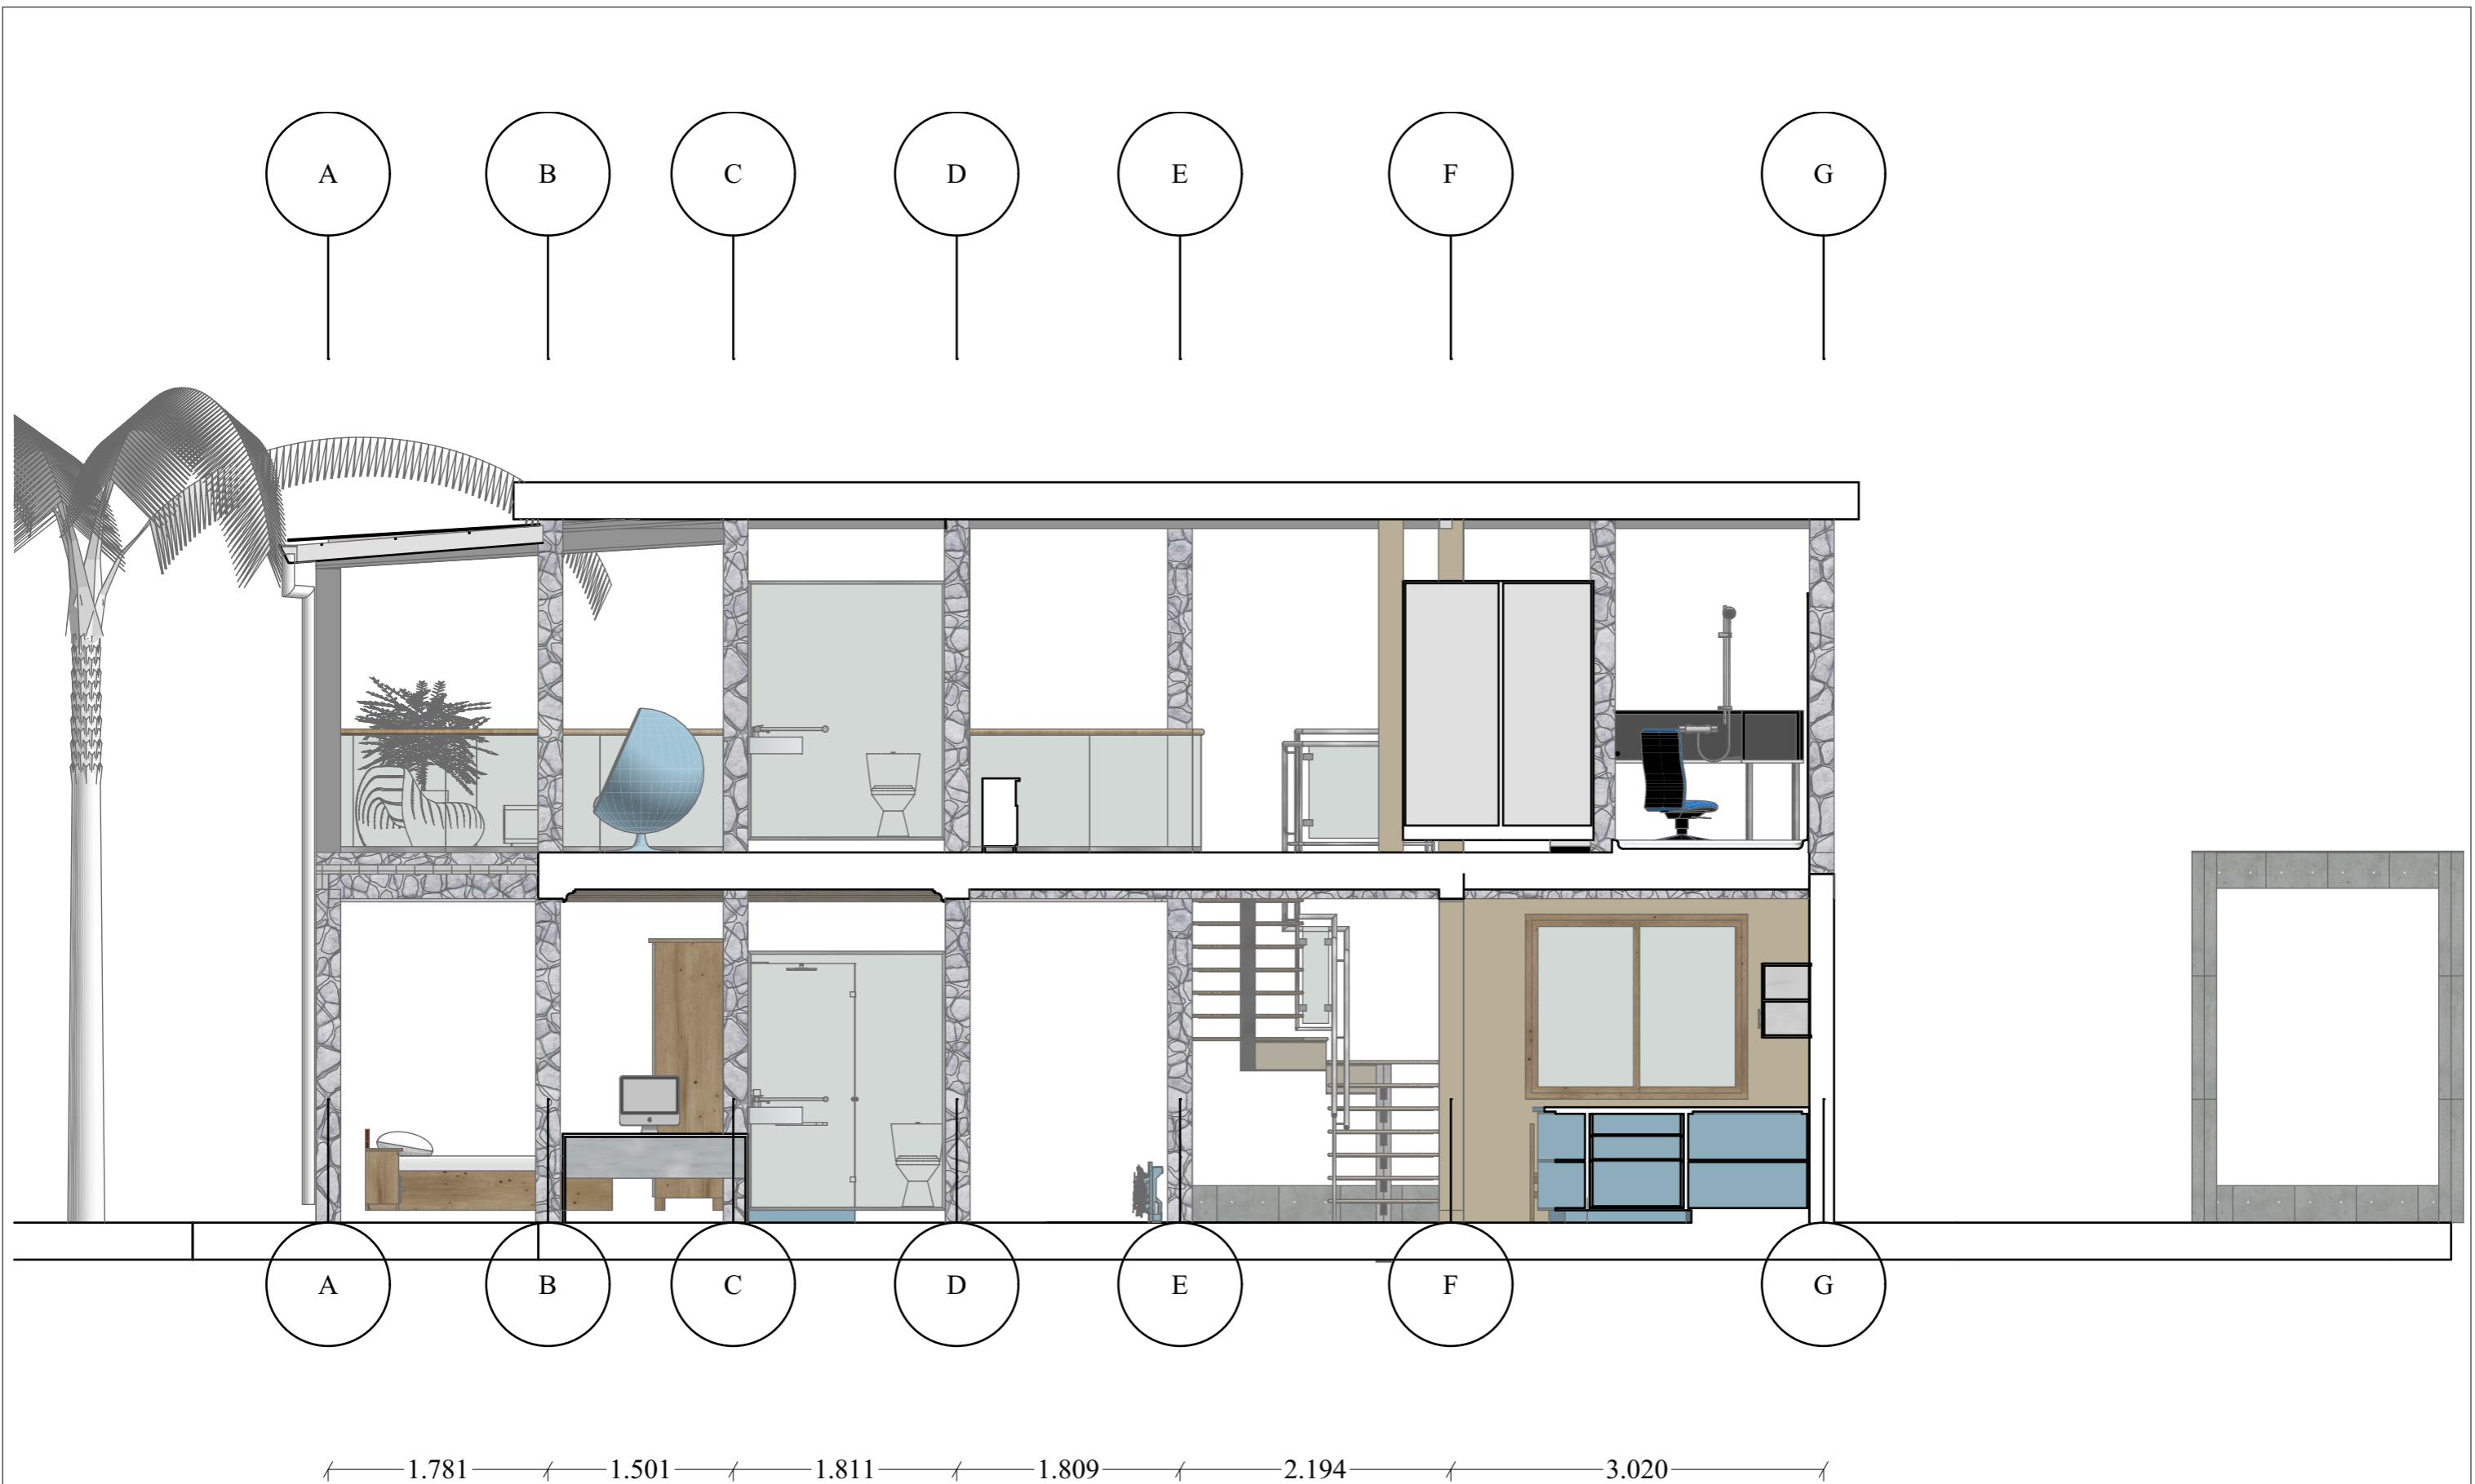

S-05

Building Section

1:50

KASHYAP HARISH VAGHANI

SCHOOL: KENCID

SCALE: 1:50

09/07/2024

REG: ARE/0171A/2023

BUILDING SECTION